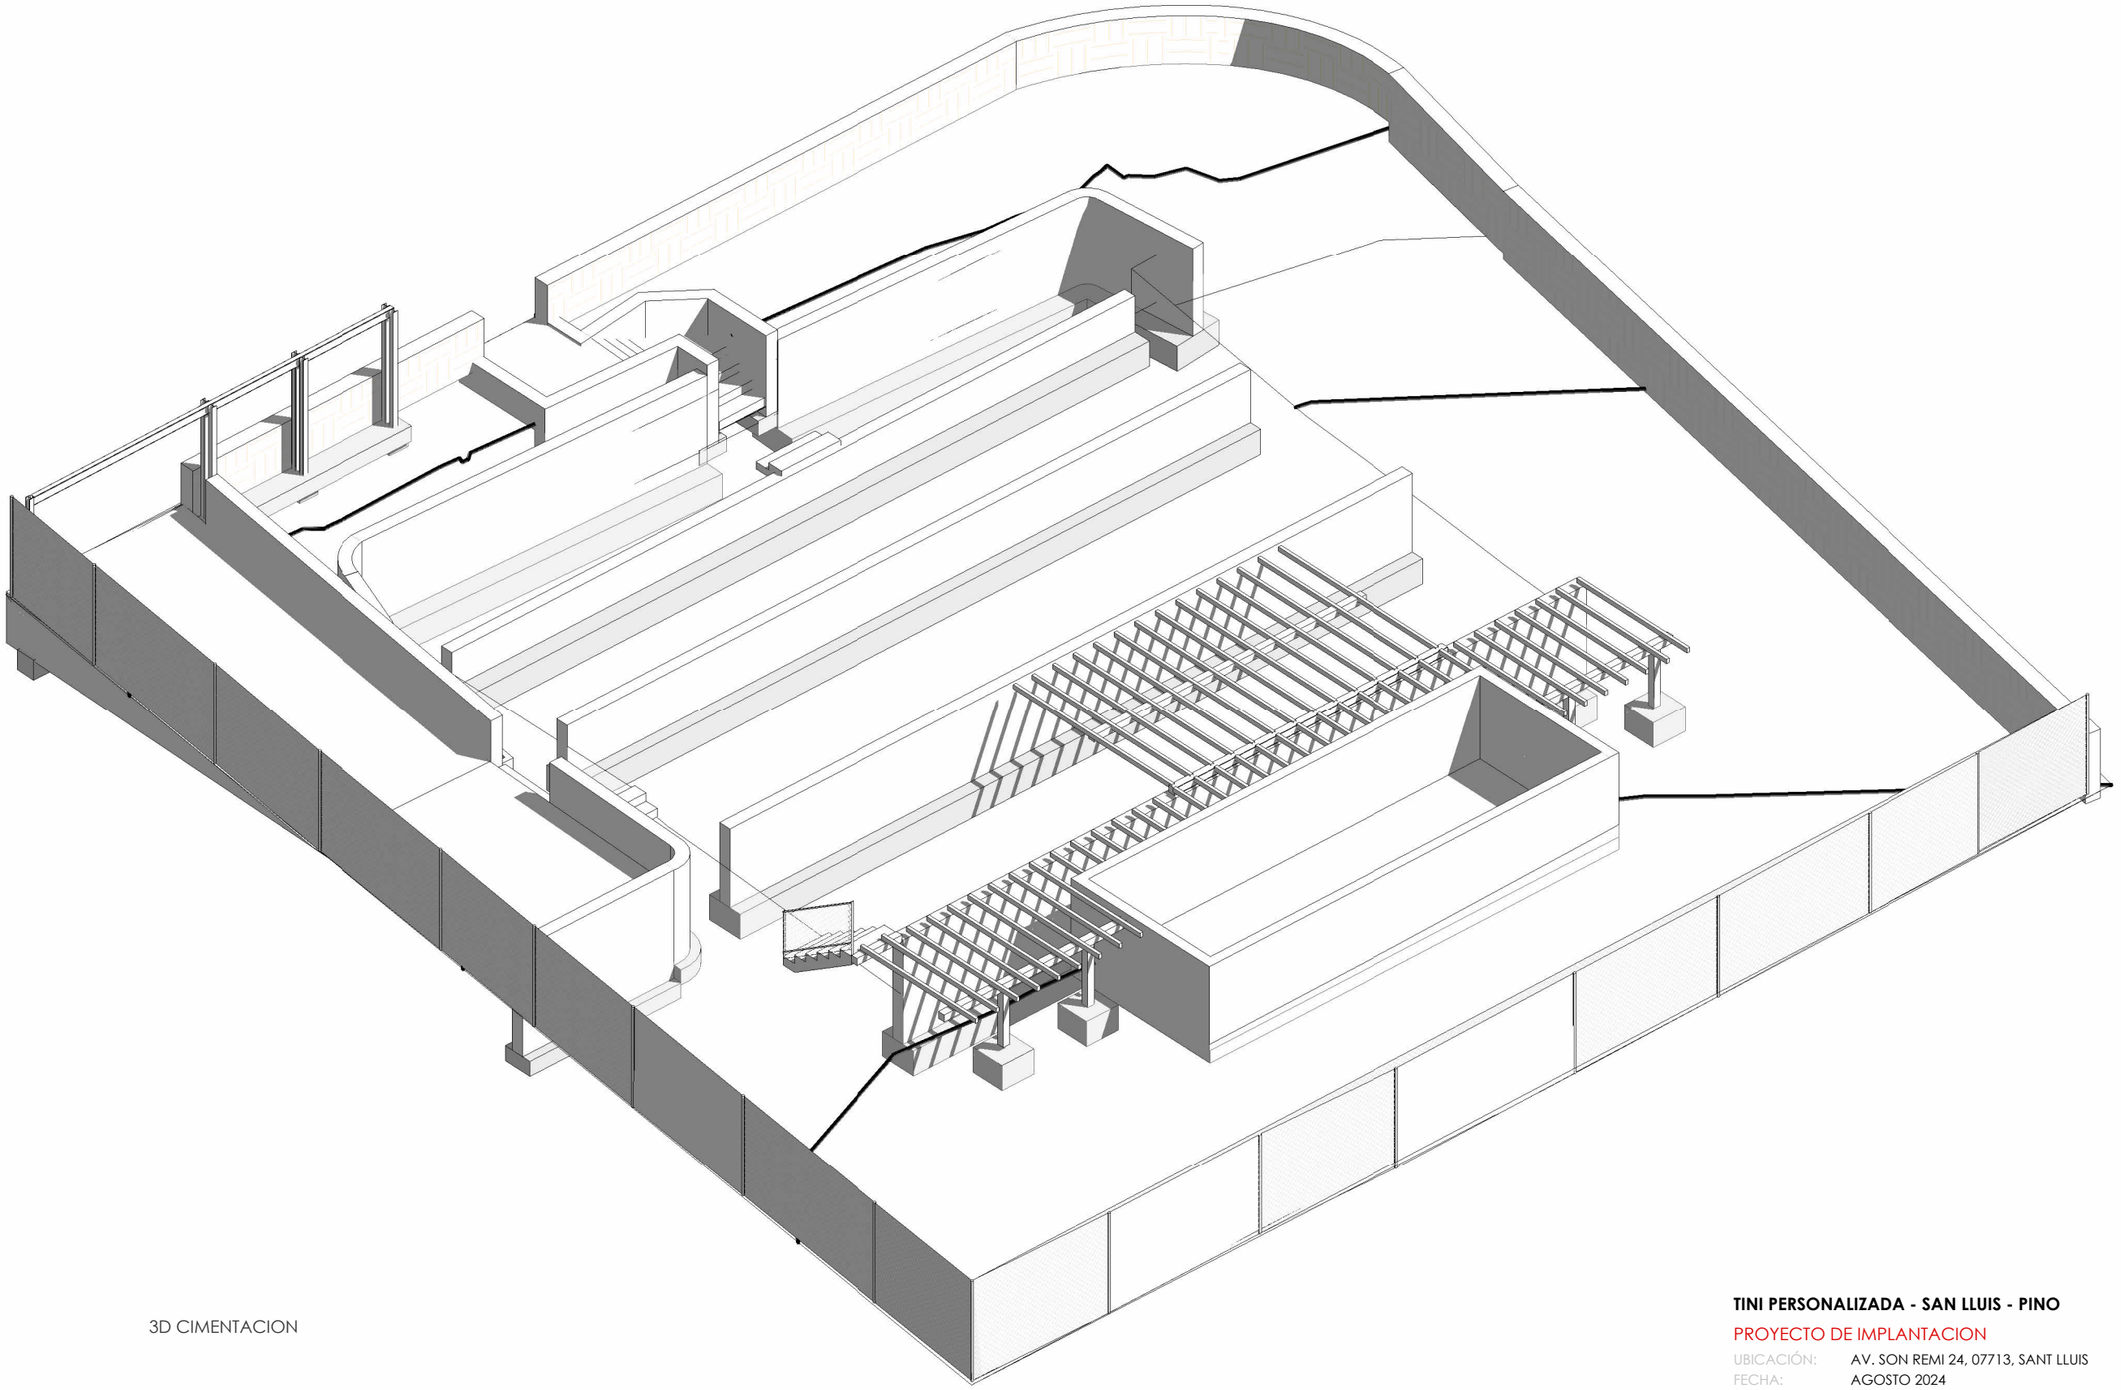


3D CIMENTACION


**TINI PERSONALIZADA - SAN LLUIS - PINO**

PROYECTO DE IMPLANTACION

UBICACIÓN: AV. SON REMI 24, 07713, SANT LLUIS
FECHA: AGOSTO 2024
ESCALA:
CAPÍTULO: ARQUITECTURA
TÍTULO: PORTADA 3D CIMENTACIONES

00

| PROPIEDAD | ARQUITECTO | FORMATO | REVISIÓN |
|---|---|---|---|
| Sr./Sra. _____ | IGNACIO DE LA VEGA<br>Nº 22.169 (COAM)<br>ignacio@tiniliving.com | A3 | Verificador |

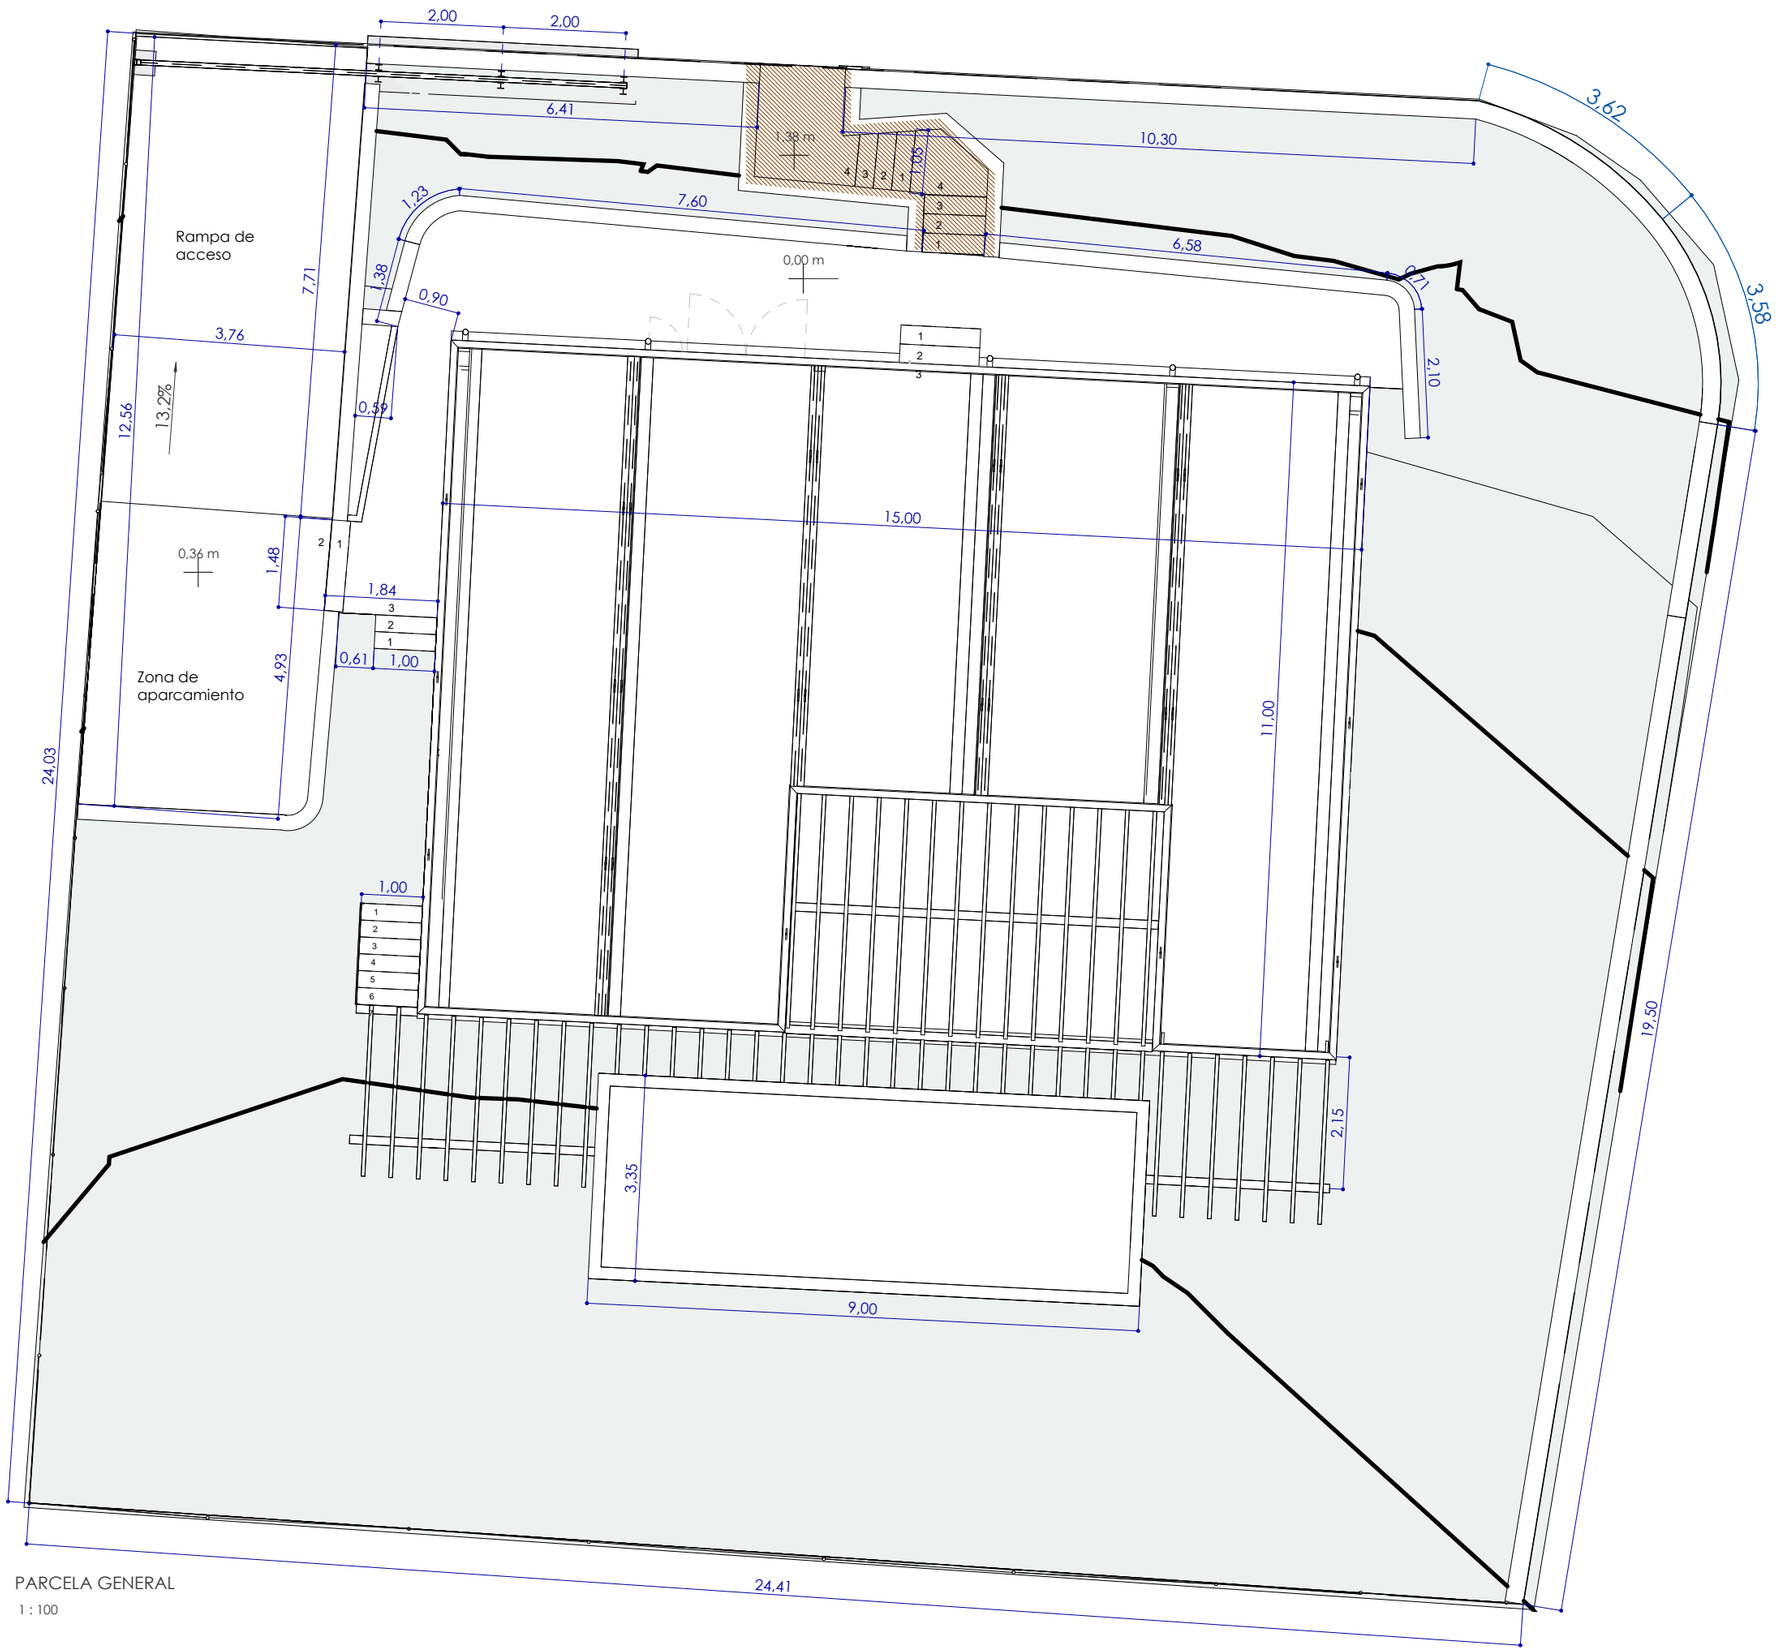


PARCELA GENERAL

1 : 100

**TINI PERSONALIZADA - SAN LLUIS - PINO**

PROYECTO DE IMPLANTACION


UBICACIÓN: AV. SON REMI 24, 07713, SANT LLUIS
FECHA: AGOSTO 2024
ESCALA: 1 : 100
CAPÍTULO: ARQUITECTURA
TÍTULO: PARCELA GENERAL

E01

| PROPIEDAD | ARQUITECTO | FORMATO | REVISIÓN |
|---|---|---|---|
| Sr./Sra. _____ | IGNACIO DE LA VEGA<br>Nº 22.169 (COAM)<br>ignacio@tiniliving.com | A3 | Verificador |




CERRAMIENTO DE PARCELA
muro de piedra mares h=0.8m

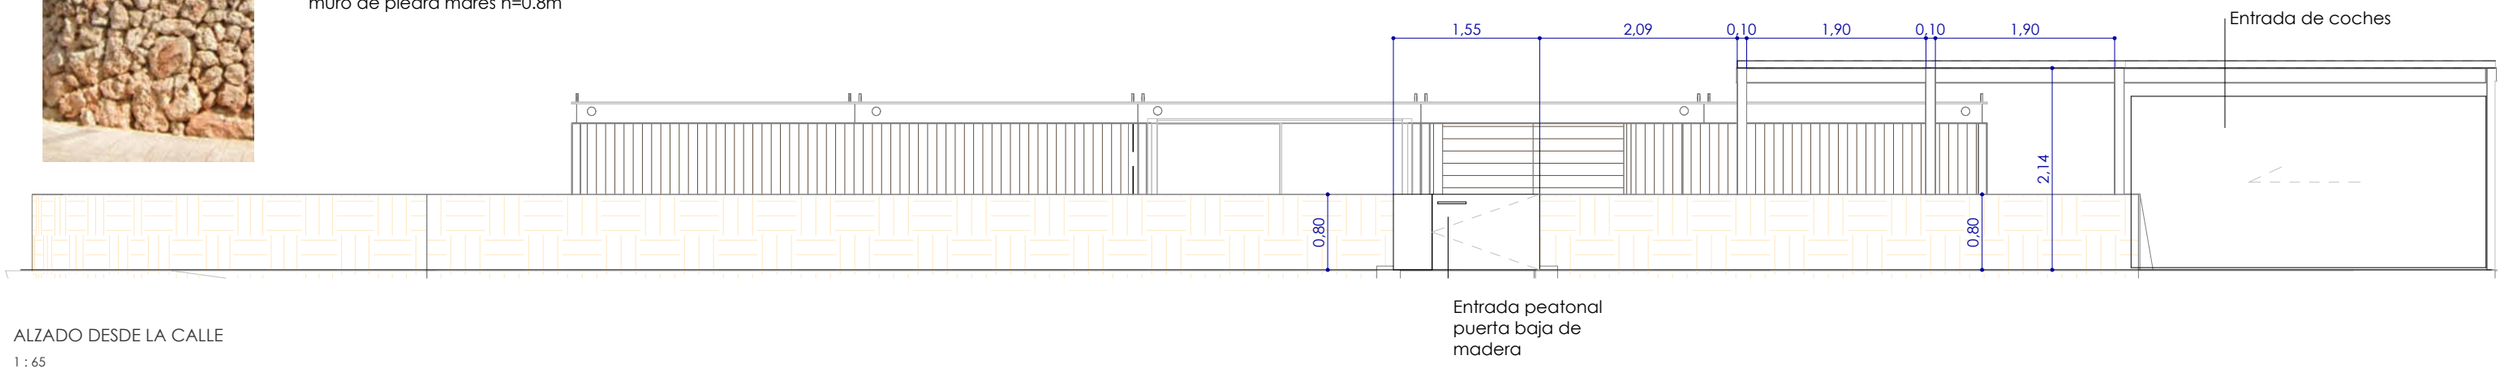


ALZADO DESDE LA CALLE

1 : 65

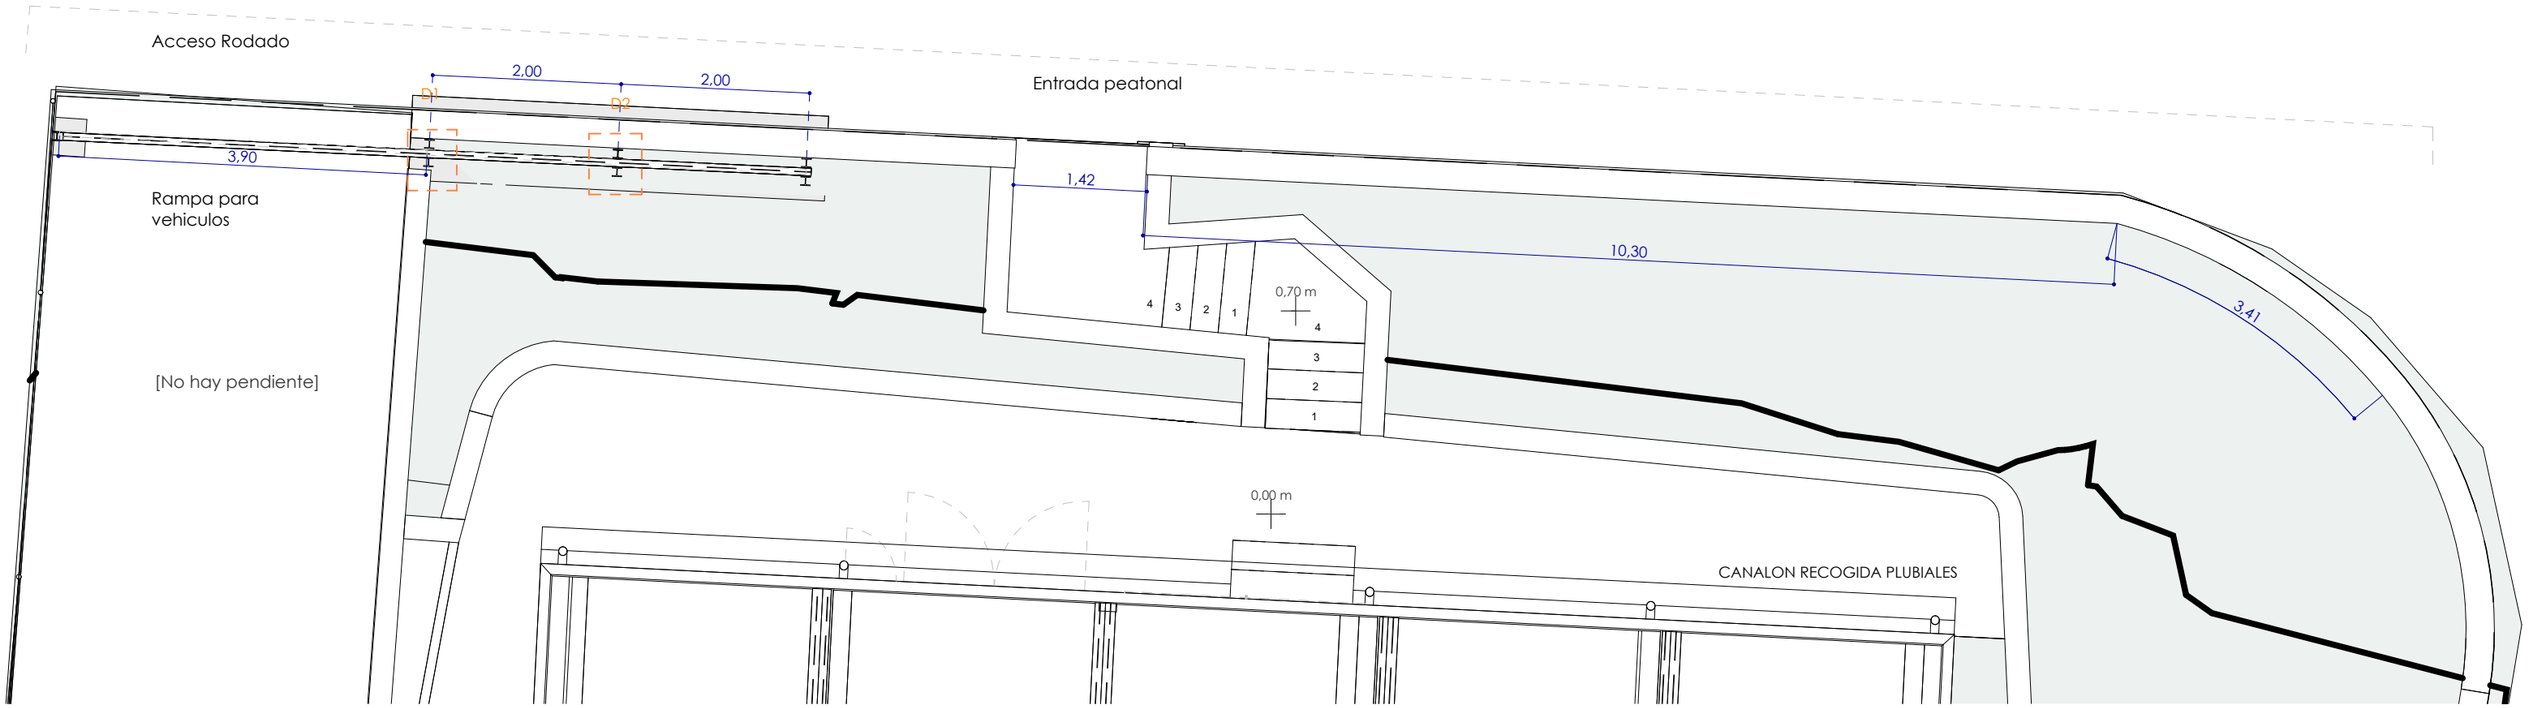


VALLADO DE PARCELA

1 : 65

**TINI PERSONALIZADA - SAN LLUIS - PINO**


PROYECTO DE IMPLANTACION

UBICACIÓN: AV. SON REMI 24, 07713, SANT LLUIS
FECHA: AGOSTO 2024
ESCALA: 1 : 65
CAPÍTULO: ARQUITECTURA
TÍTULO: CERRAMIENTO DE PARCELA


E02

| PROPIEDAD | ARQUITECTO | FORMATO | REVISIÓN |
|---|---|---|---|
| Sr./Sra. _____ | IGNACIO DE LA VEGA<br>Nº 22.169 (COAM)<br>ignacio@finilliving.com | A3 | Verificador |

Acceso Rodado

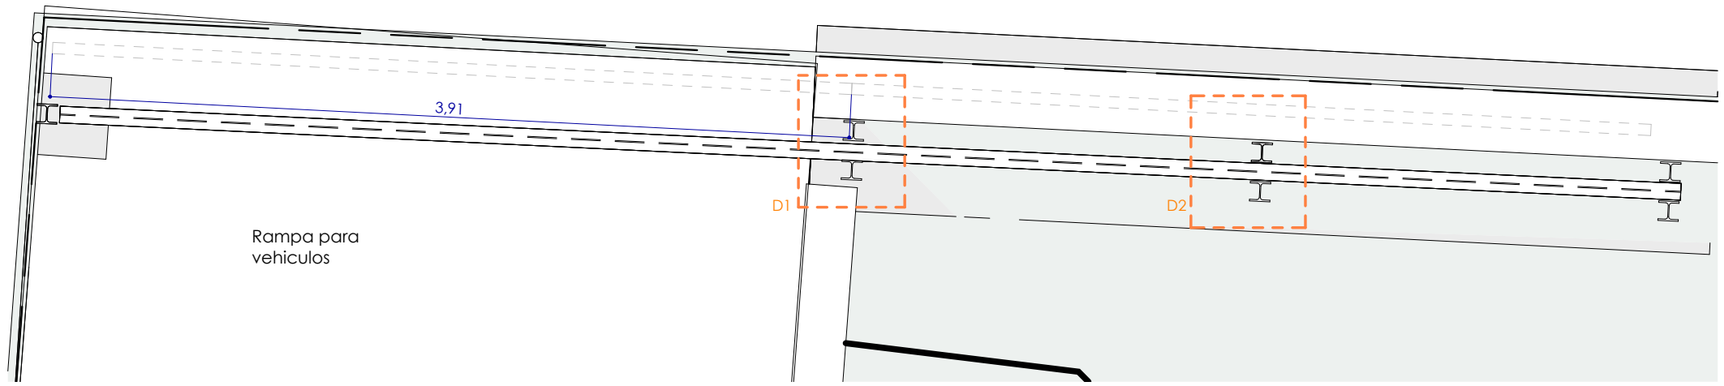



Entrada peatonal

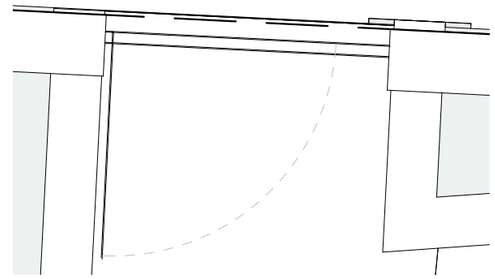

VALLADO DE PARCELA DETALLE


1 : 30


D1

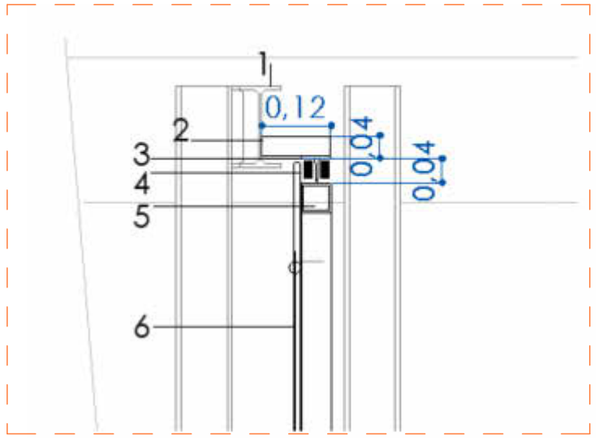


1-VIGA SUPERIOR IPE120
2-PERFIL T INVERTIDO DE 35X35
3-PERFIL T DE 35X35
4-RODAMIENTO
5-BASTIDOR DE TUBO 50.3
6-PUERTA DE CHAPA LISA DE 1MM
7-RODAMIENTO  CARRIL INFERIOR
8-ZAPATA CORRIDA DE MURO

D2

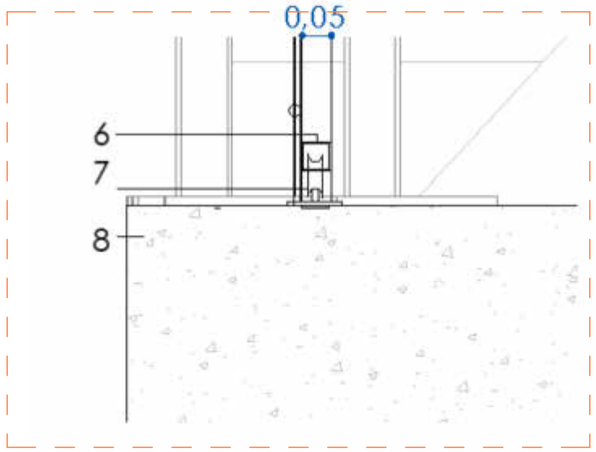

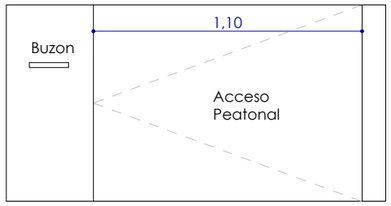
DETALLE ENTRADA PEATONAL

1 : 25


**TINI PERSONALIZADA - SAN LLUIS - PINO**

PROYECTO DE IMPLANTACION

UBICACIÓN: AV. SON REMI 24, 07713, SANT LLUIS
FECHA: AGOSTO 2024
ESCALA: Como se indica
CAPÍTULO: ARQUITECTURA
TÍTULO: CERRAMIENTO DETALLE

E02.1


| PROPIEDAD | ARQUITECTO | FORMATO | REVISIÓN |
|---|---|---|---|
| Sr./Sra. _____ | IGNACIO DE LA VEGA<br>Nº 22.169 (COAM)<br>ignacio@tiniliving.com | A3 | Verificador |

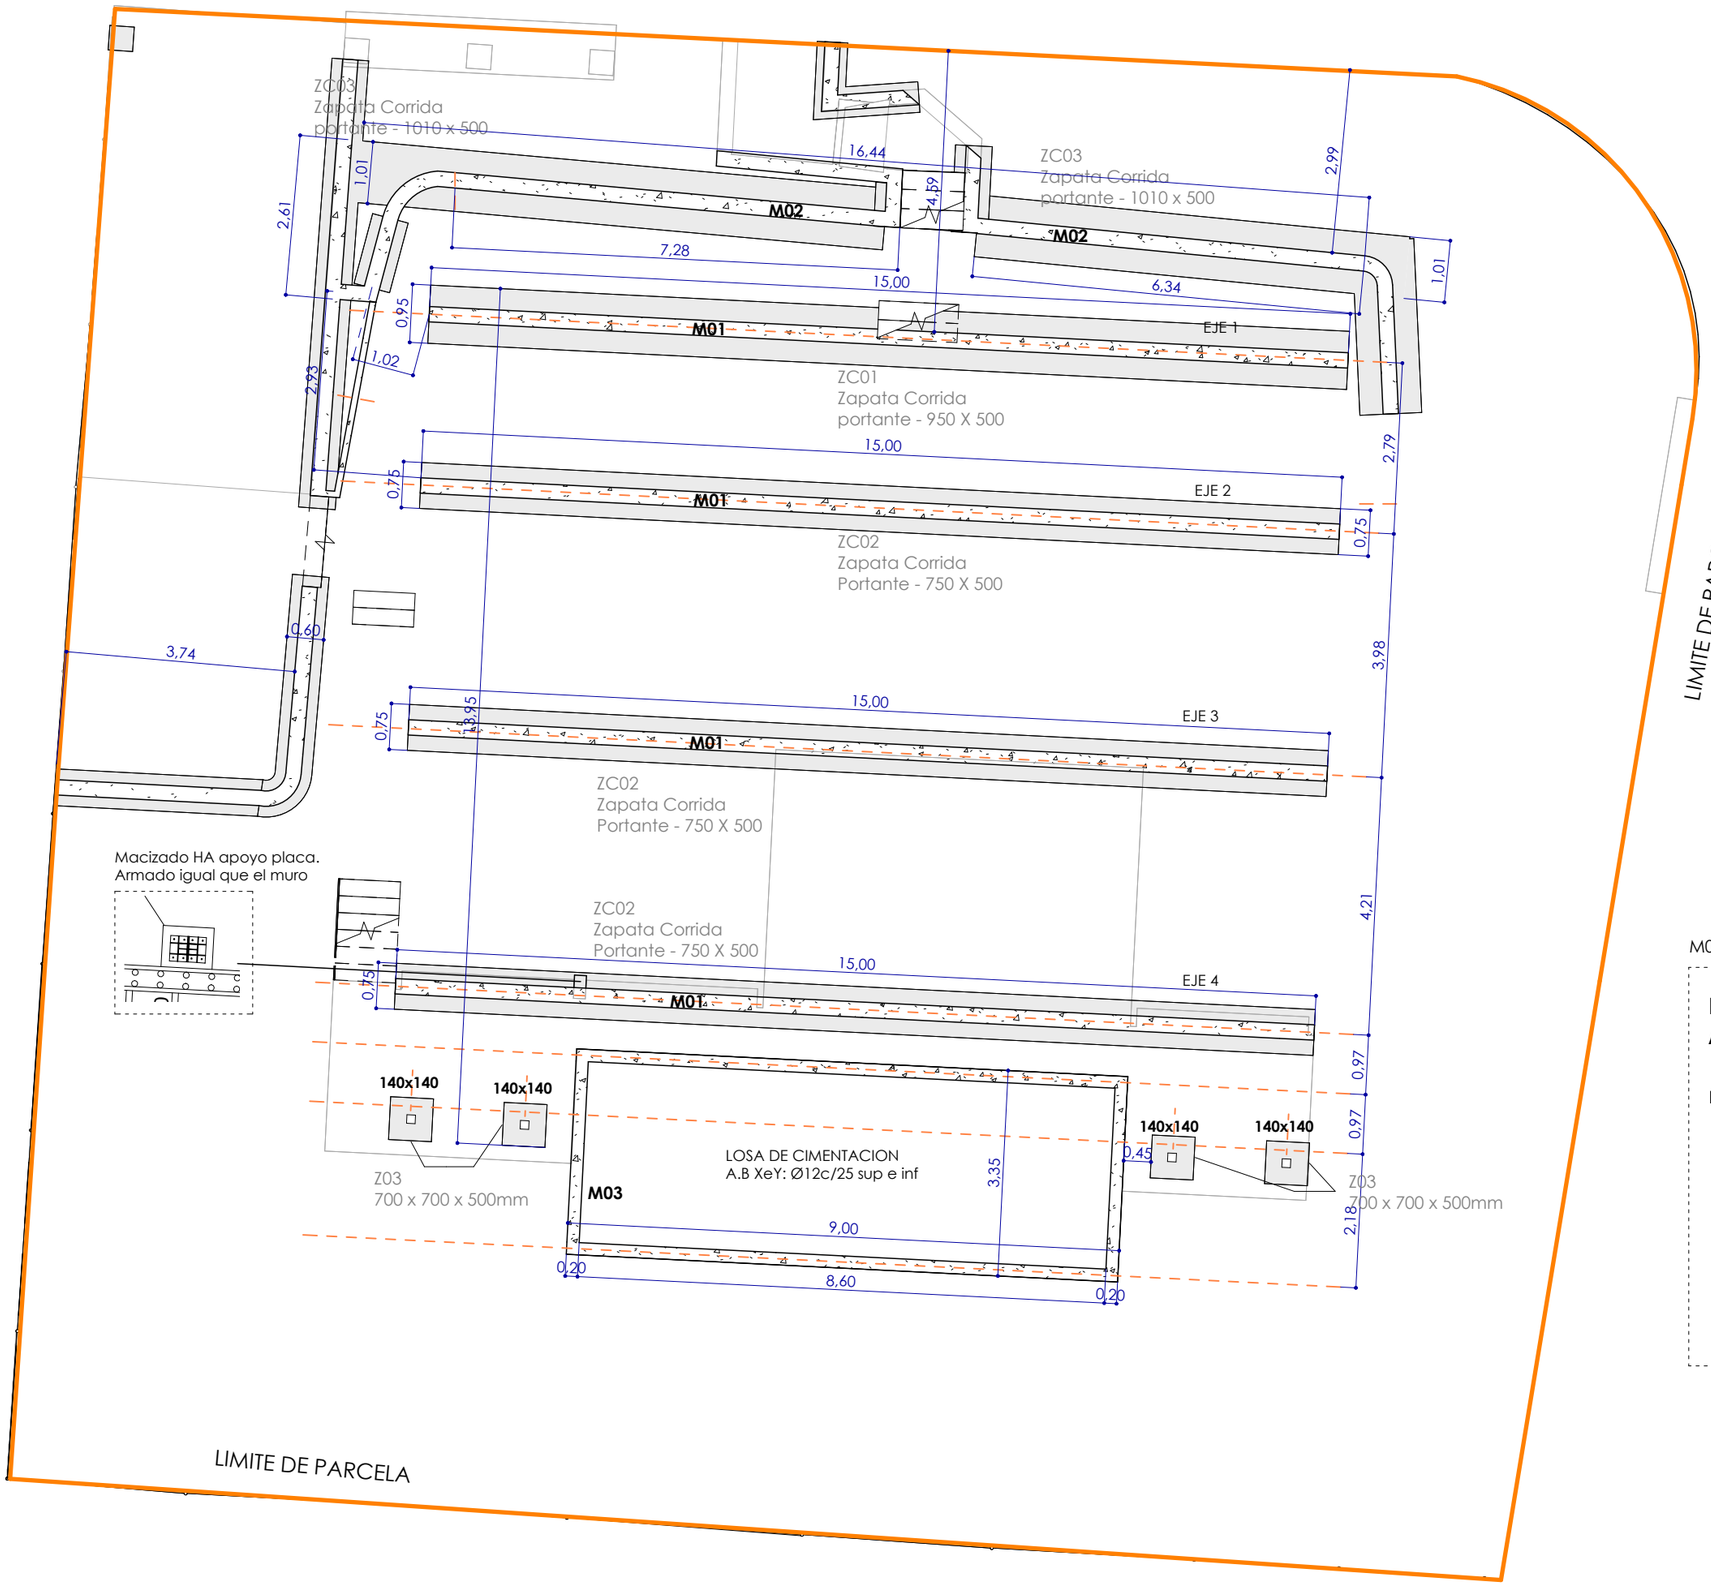



Nivel CIMENTACION

1 : 100


ZC02

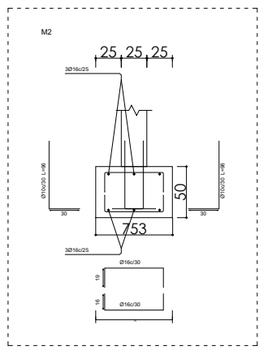


ZC01

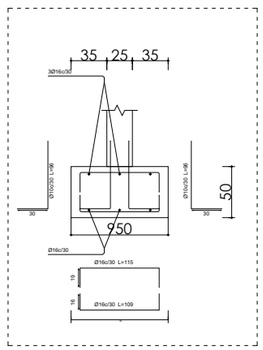



M01

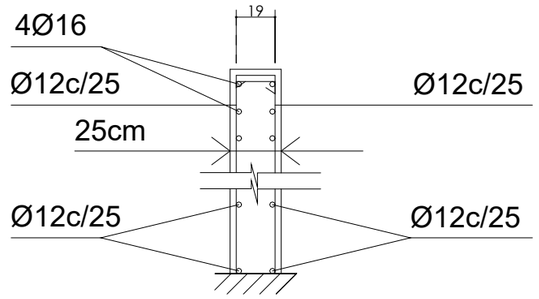



M02 y ZC03

Muro

Armadura

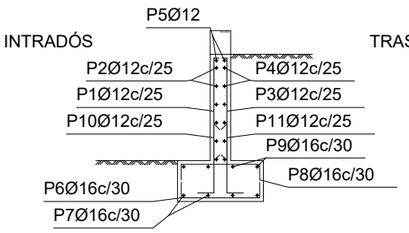


Geometría

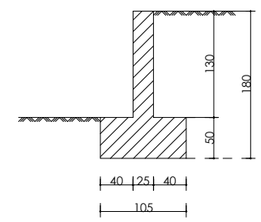



**TINI PERSONALIZADA - SAN LLUIS - PINO**

PROYECTO DE IMPLANTACION

UBICACIÓN: AV. SON REMI 24, 07713, SANT LLUIS
FECHA: AGOSTO 2024
ESCALA: Como se indica
CAPÍTULO: ARQUITECTURA
TÍTULO: CIMENTACION


E03

| PROPIEDAD | ARQUITECTO | FORMATO | REVISIÓN |
|---|---|---|---|
| Sr./Sra. _____ | IGNACIO DE LA VEGA<br>Nº 22.169 (COAM)<br>ignacio@tiniliving.com | A3 | Verificador |

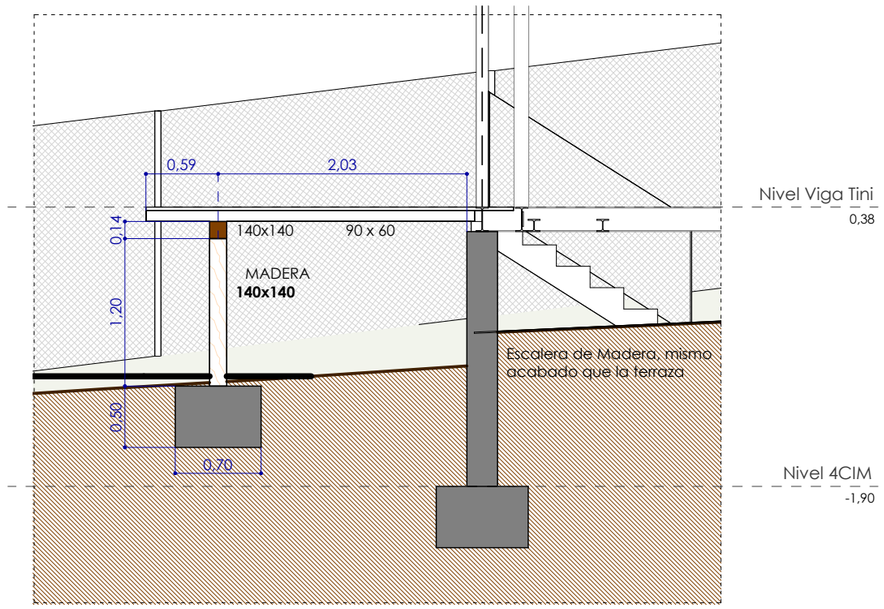



CIMENTACION TERRAZA

1 : 50

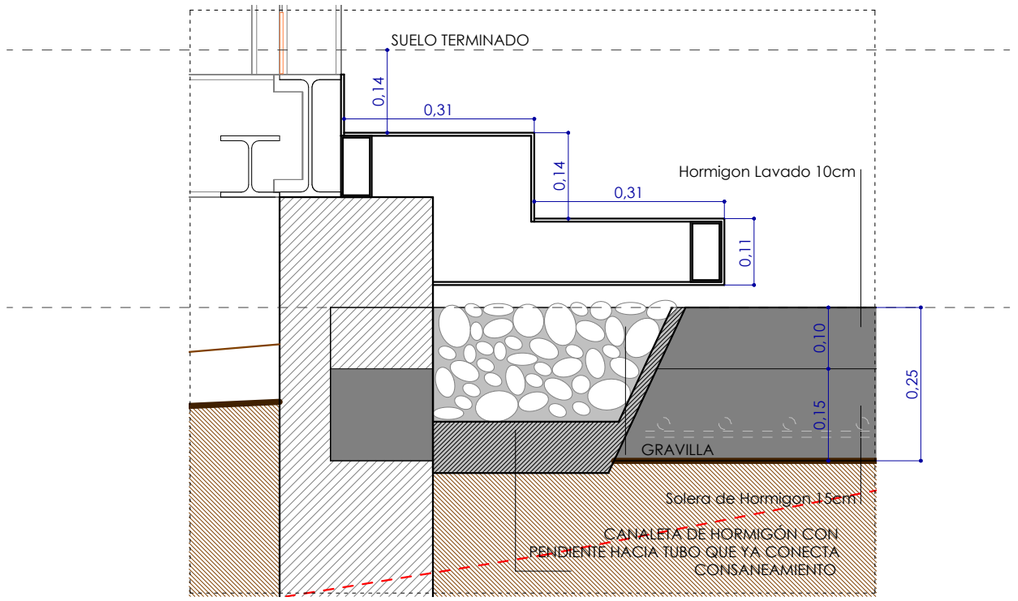


DETALLE ACCESO VIVIENDA

1 : 10

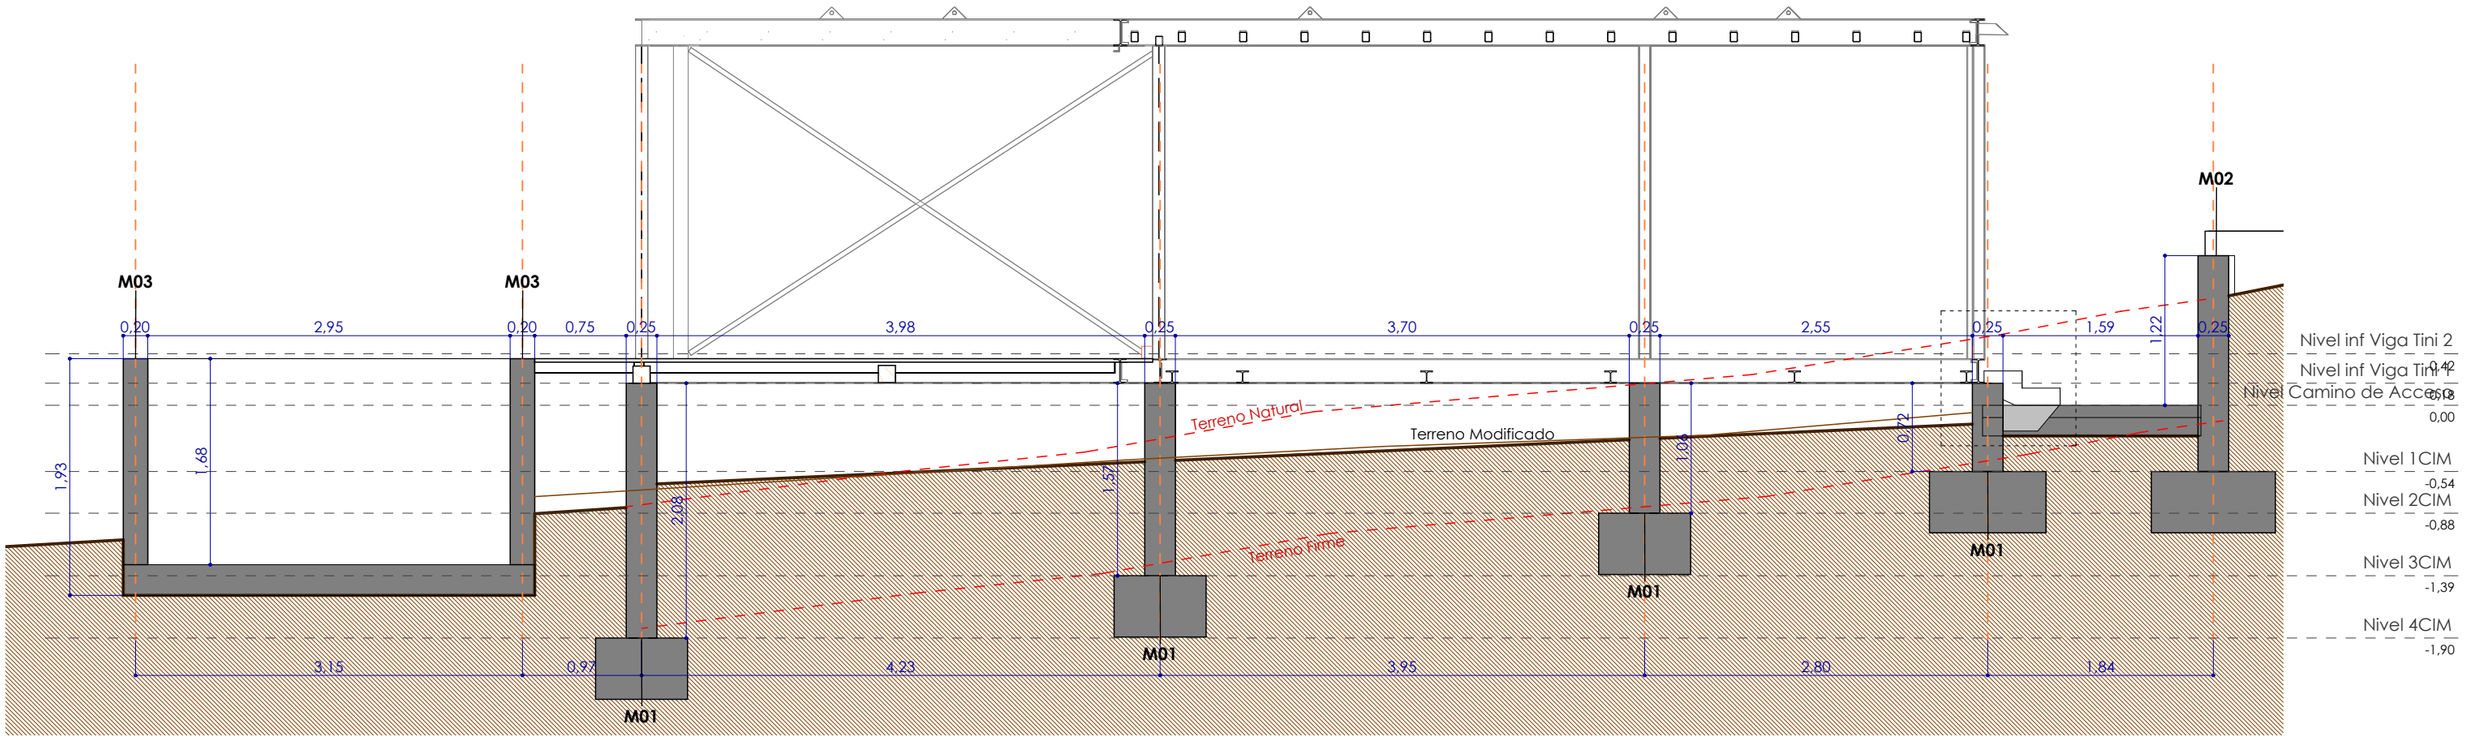


SECCION CIMENTACION PISCINA

1 : 50


**TINI PERSONALIZADA - SAN LLUIS - PINO**

PROYECTO DE IMPLANTACION

UBICACIÓN: AV. SON REMI 24, 07713, SANT LLUIS
FECHA: AGOSTO 2024
ESCALA: Como se indica
CAPÍTULO: ARQUITECTURA
TÍTULO: SECCIONES GENERALES


E04

| PROPIEDAD | ARQUITECTO | FORMATO | REVISIÓN |
|---|---|---|---|
| Sr./Sra. _____ | IGNACIO DE LA VEGA<br>Nº 22.169 (COAM)<br>ignacio@tiniliving.com | A3 | Verificador |

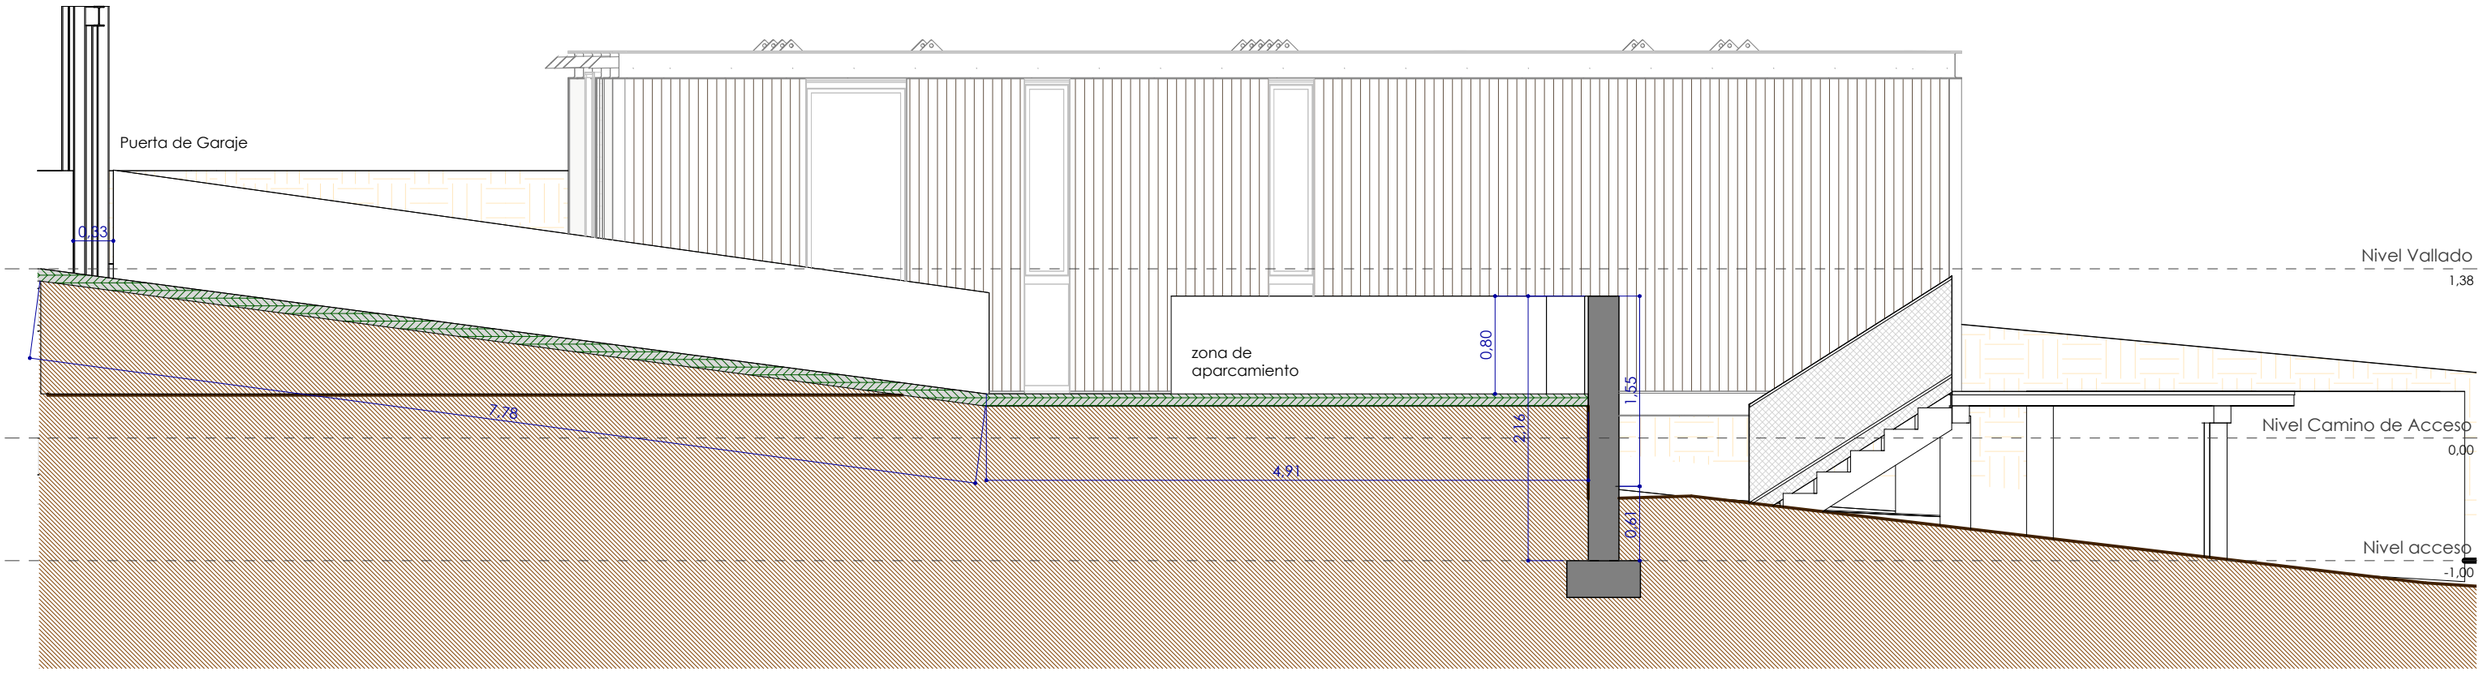



ZONA APARCAMIENTO

1 : 50

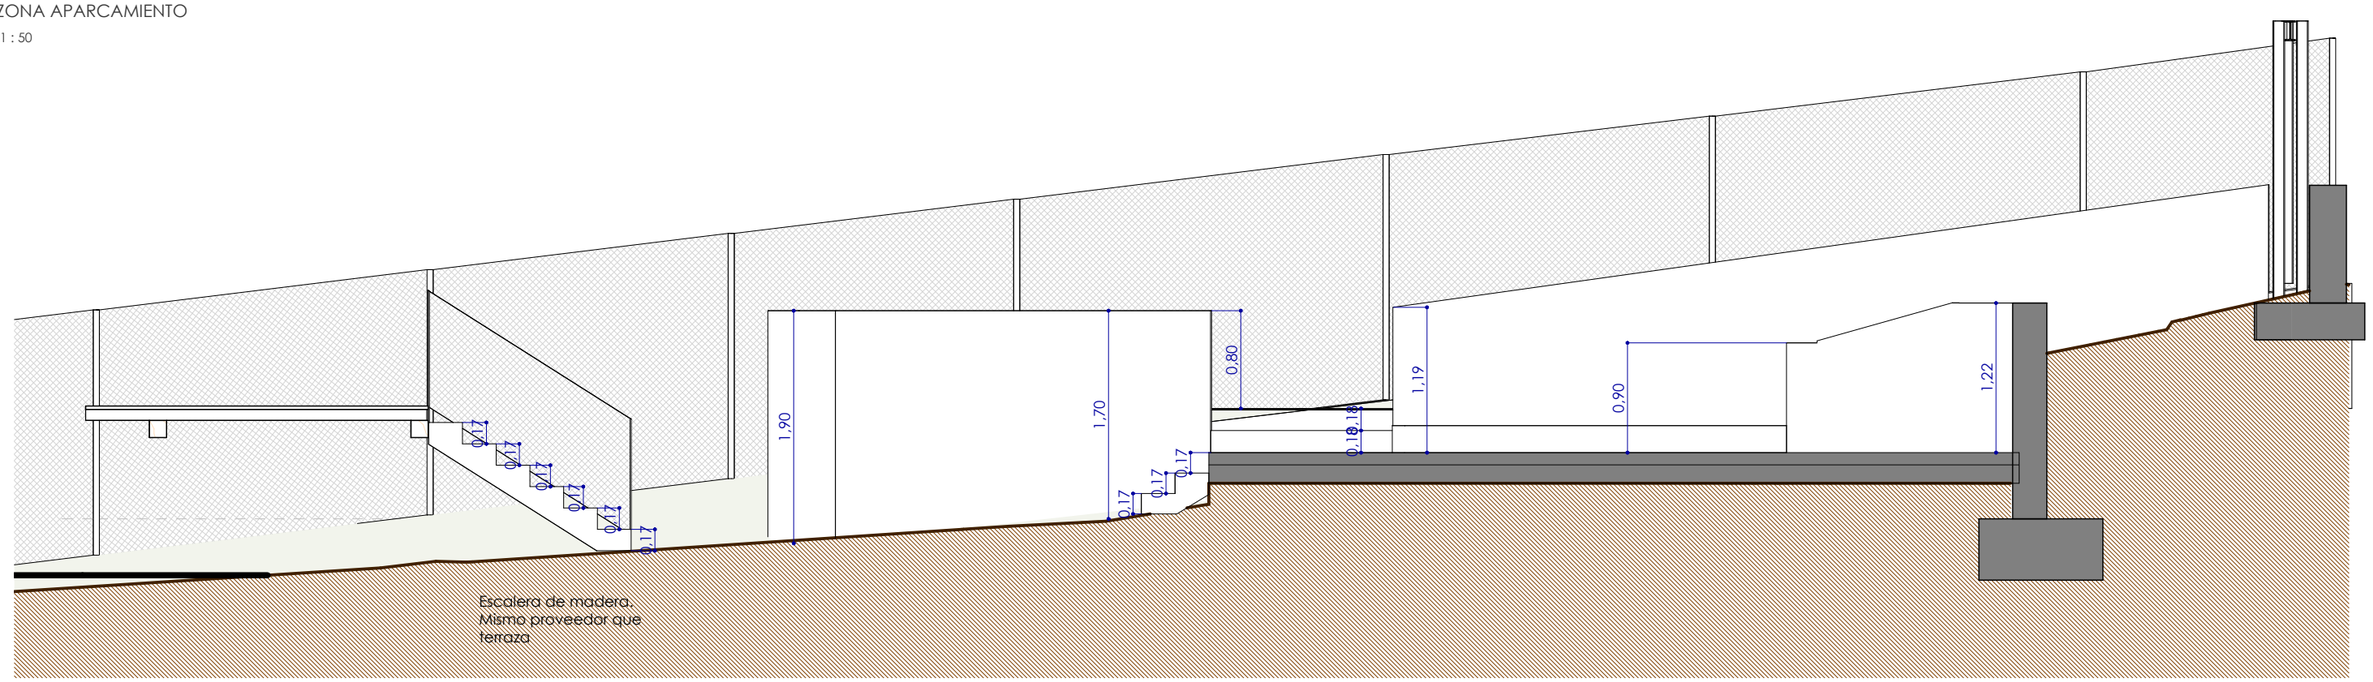


ZONA ACCESO TERRAZA

1 : 50

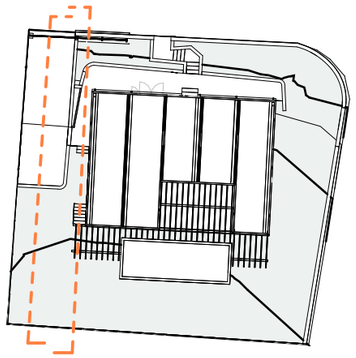


**TINI PERSONALIZADA - SAN LLUIS - PINO**

PROYECTO DE IMPLANTACION

| | |
|---|---|
| UBICACIÓN: | AV. SON REMI 24, 07713, SANT LLUIS |
| FECHA: | AGOSTO 2024 |
| ESCALA: | Como se indica |
| CAPÍTULO: | ARQUITECTURA |
| TÍTULO: | SECCIONES PARCELA 1 |


E04.2

| PROPIEDAD | ARQUITECTO | FORMATO | REVISIÓN |
|---|---|---|---|
| Sr./Sra. _____ | IGNACIO DE LA VEGA<br>Nº 22.169 (COAM)<br>ignacio@tiniliving.com | A3 | Verificador |

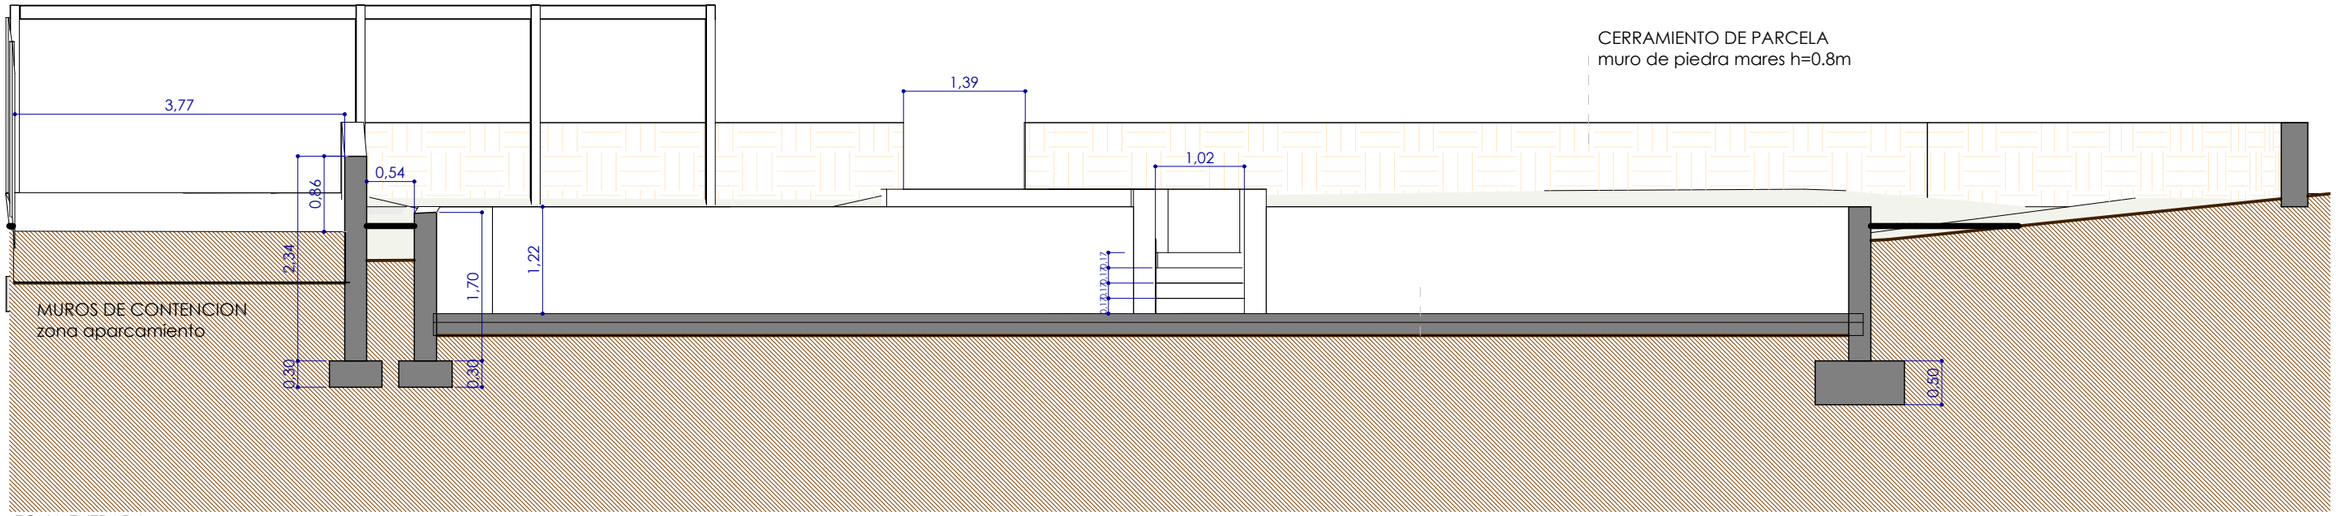



ZONA ENTRADA

1 : 70

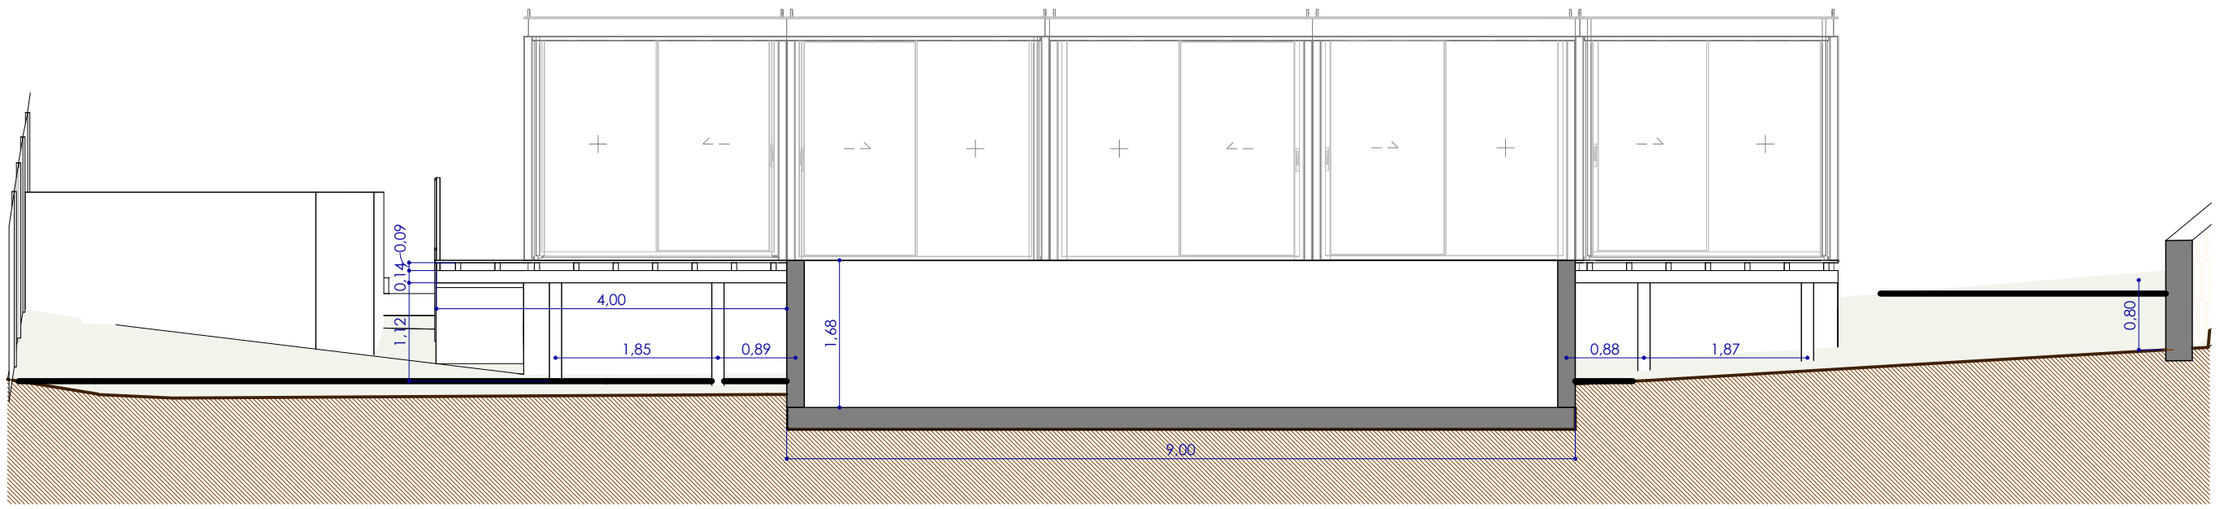


SECCION GENERAL 2

1 : 70

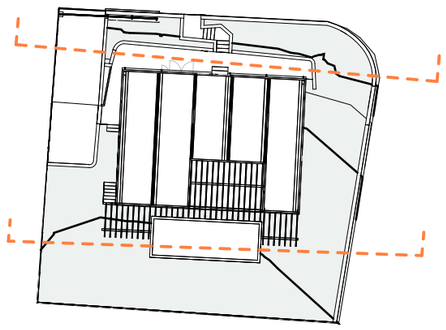


**TINI PERSONALIZADA - SAN LLUIS - PINO**

PROYECTO DE IMPLANTACION

UBICACIÓN: AV. SON REMI 24, 07713, SANT LLUIS
FECHA: AGOSTO 2024
ESCALA: Como se indica
CAPÍTULO: ARQUITECTURA
TÍTULO: SECCIONES PARCELA 2

E04.3

| PROPIEDAD | ARQUITECTO | FORMATO | REVISIÓN |
|---|---|---|---|
| Sr./Sra. _____ | IGNACIO DE LA VEGA<br>Nº 22.169 (COAM)<br>ignacio@tiniliving.com | A3 | Verificador |

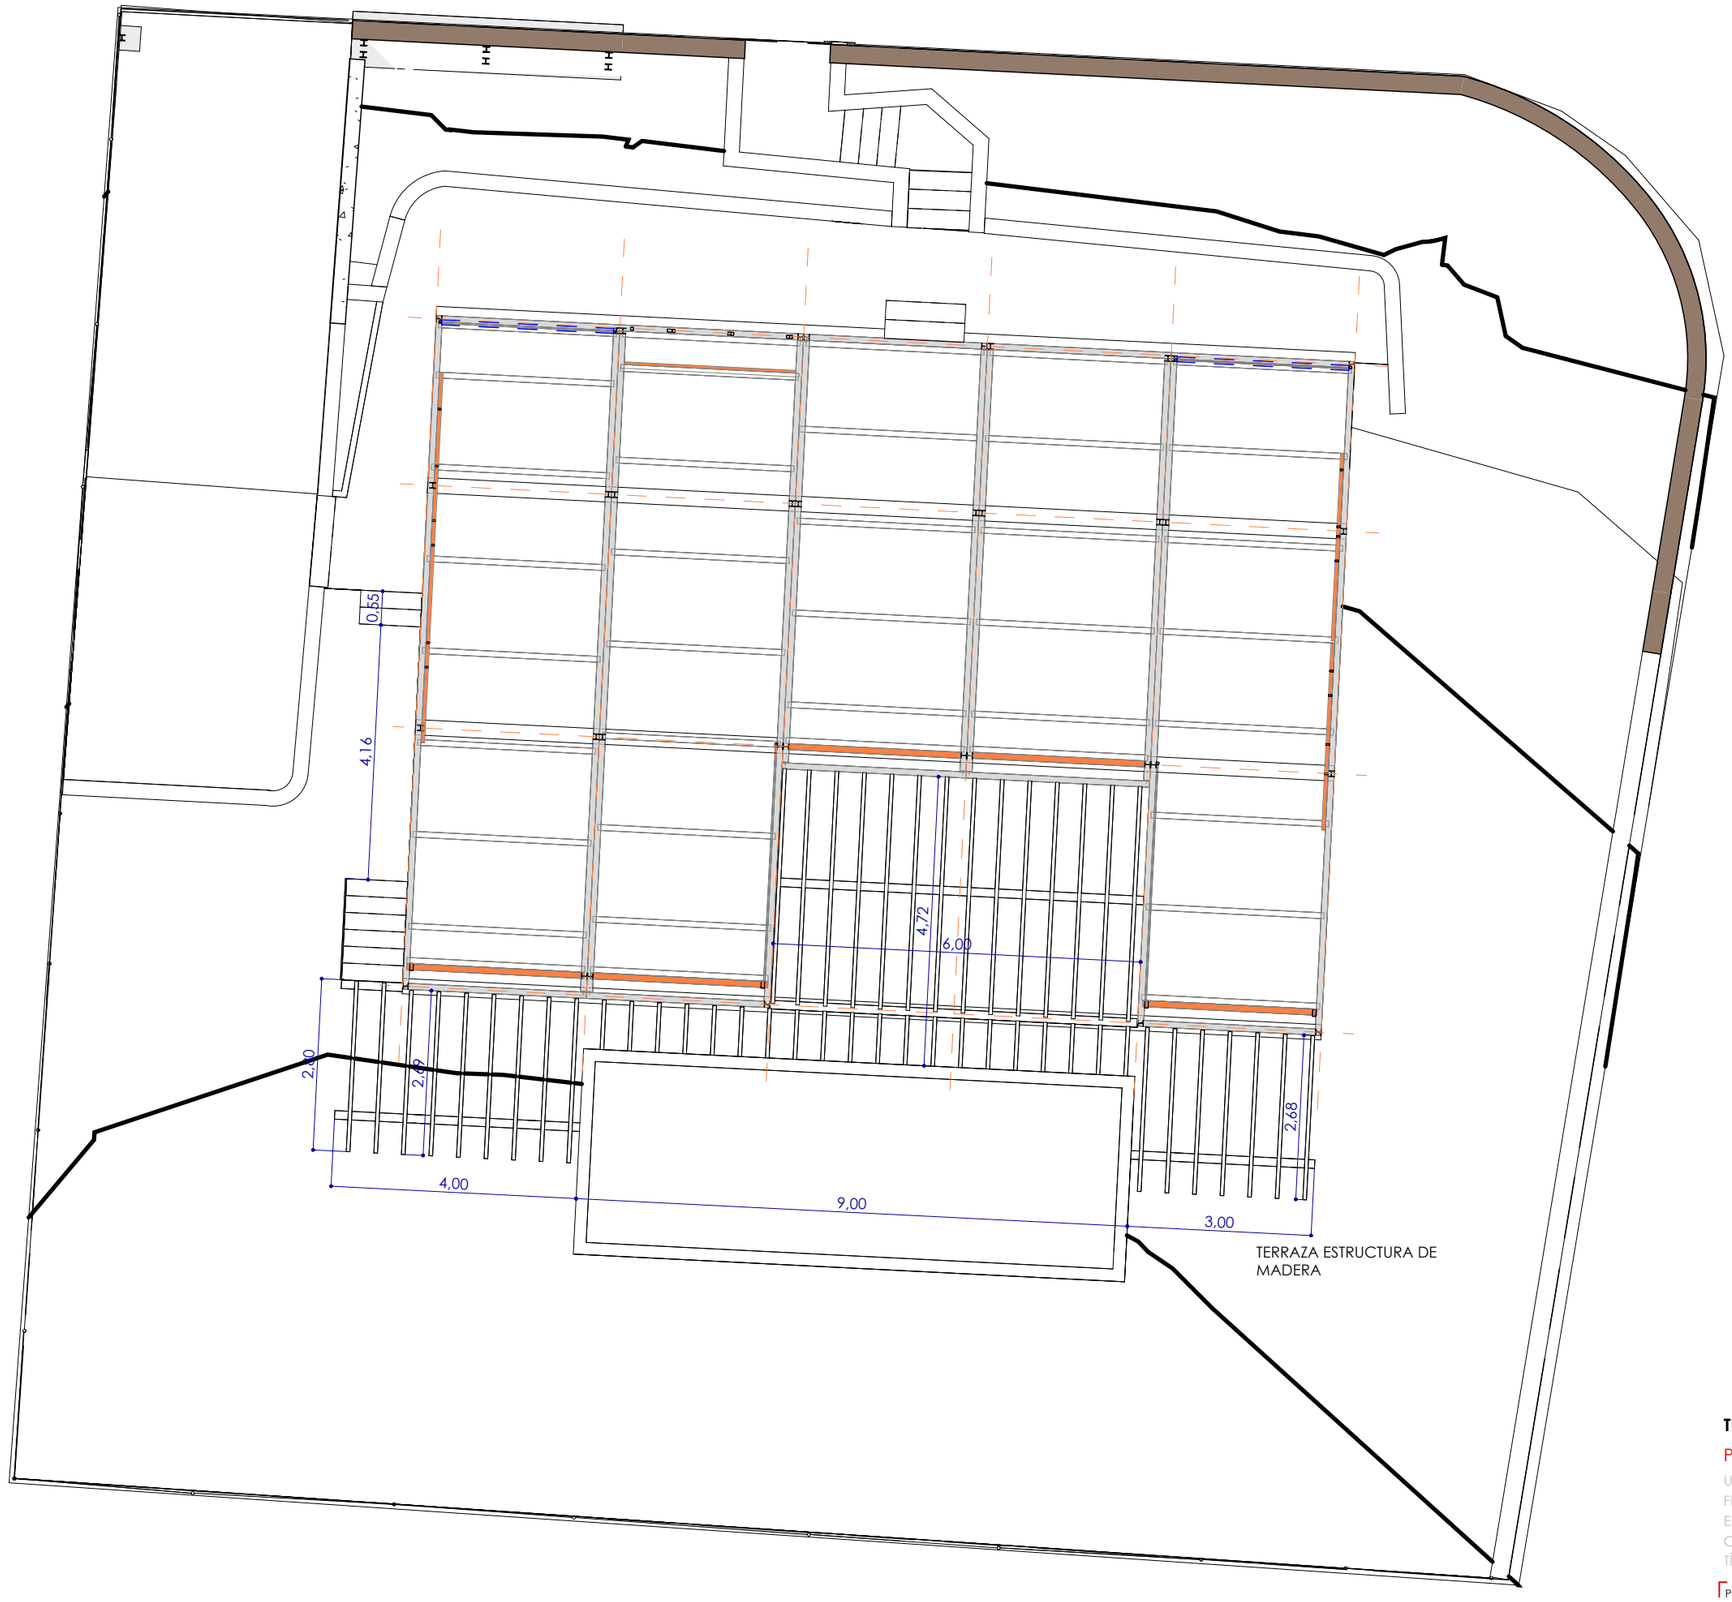


Nivel TERRAZA

1 : 100

**TINI PERSONALIZADA - SAN LLUIS - PINO**

PROYECTO DE IMPLANTACION

UBICACIÓN: AV. SON REMI 24, 07713, SANT LLUIS
FECHA: AGOSTO 2024
ESCALA: 1 : 100
CAPÍTULO: ARQUITECTURA
TÍTULO: ESTRUCTURA

E05

| PROPIEDAD | ARQUITECTO | FORMATO | REVISIÓN |
|---|---|---|---|
| Sr./Sra. _____ | IGNACIO DE LA VEGA<br>Nº 22.169 (COAM)<br>ignacio@tiniliving.com | A3 | Verificador |

# CUADRO DE CARACTERISTICAS CÓDIGO ESTRUCTURAL

## CARACTERISTICAS GENERALES DE TODA LA OBRA


| | |
|---|---|
| TIPO DE ESTRUCTURA Y VIDA ÚTIL (Art. 5.1.1) (ANEJO 18 - Apartado 2.3 Vida útil) | Estructuras de edificación y otras estructuras comunes |
| | 50 años |
| CONTROL DE EJECUCIÓN (Art. 14.3 - Art. 22.4) | Normal |
| TENSIÓN ADMISIBLE DEL TERRENO | 0,46 MPa (4,60 Kp/cm²) |

## CARACTERISTICAS DEL HORMIGÓN

| ELEMENTOS ESTRUCTURALES | TIPO DE HORMIGON (2) | CONSISTENCIA ASENTAMIENTO | NIVEL DE CONTROL | COEFICIENTES (Anejo 19 - 2.4.2.4) | | RECUBRIMIENTO NOMINAL (Anejo 19 - 4.4.1) | | |
|---|---|---|---|---|---|---|---|---|
| | | | | Persistente | Accidental | Cnom = ΔCdev + Cmin (Art. 43.4.1) (Art. 43.4.1 + Art. 44.2.1, 44.3, 44.4.4-44.5) | | |
| TODA LA OBRA | | | | | | | | |
| CIMENTACIÓN Y MUROS (1) | HA-25/F/20/XC2 | 100-150 | Estadístico | 1,50 | 1,30 | 30 mm / 70 mm (1) | 10 mm | 20 mm |

(1) Para piezas hormigonadas contra el terreno el recubrimiento mínimo es de 70 mm (Art. 44.2.1)
(2) En obras de edificación, para pilares, forjados y vigas se utilizará un hormigón de consistencia fluida (F) salvo justificación en contra (Art. 33.5)

### Recubrimientos nominales

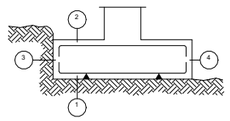


1a.- Recubrimiento inferior contacto terreno ≥ 8 cm.
1b.- Recubrimiento con hormigón de limpieza 4 cm.
2.- Recubrimiento superior libre 4/5 cm.
3.- Recubrimiento lateral contacto terreno ≥ 8 cm.
4.- Recubrimiento lateral libre 4/5 cm.

## CARACTERISTICAS DEL ACERO

| ELEMENTOS ESTRUCTURALES | ACEROS PARA ARMADURAS PASIVAS (Art. 34 y 35) | | | | ACERO LAMINADO | COEFICIENTES (Anejo 19 - 2.4.2.4) | |
|---|---|---|---|---|---|---|---|
| | Barras y rollos de acero corrugado | | Alambres corrugados y lisos | | | Persistente | Accidental |
| TODA LA OBRA | B 500 S | Marcado CE | B 500 S | Marcado CE | S 275 (UNE-EN 10025-2) | 1,15 | 1,00 |
| CIMENTACIÓN Y MUROS | B 500 S | Marcado CE | B 500 S | Marcado CE | S 275 (UNE-EN 10025-2) | 1,15 | 1,00 |
| PILARES | B 500 S | Marcado CE | B 500 S | Marcado CE | S 275 (UNE-EN 10025-2) | 1,15 | 1,00 |
| JÁCENAS | B 500 S | Marcado CE | B 500 S | Marcado CE | S 275 (UNE-EN 10025-2) | 1,15 | 1,00 |
| LOSAS Y FORJADOS | B 500 S | Marcado CE | B 500 S | Marcado CE | S 275 (UNE-EN 10025-2) | 1,15 | 1,00 |

En relación con el control del acero para las armaduras pasivas, cuando la conformidad del este disponga de marcado CE se comprobará mediante la verificación documental que los valores declarados en los documentos permiten deducir el cumplimiento de las especificaciones contempladas en el proyecto y en el artículo 34 del Código Estructural.

En los casos en los que los productos no dispongan un distintivo de calidad oficialmente reconocido conforme al artículo 18:
- Suministros de menos de 300 t:
  - División del suministro en lotes de máximo 30 t, tomando dos probetas para ensayar.
- Suministros iguales o superiores a 300 t:
  - Determinación de composición química sobre uno de cada cuatro lotes.
  - División del suministro en lotes de máximo 30 t, tomando cinco probetas para ensayar.

## DISPOSICIÓN DE SEPARADORES (Art. 49.8.2)

| ELEMENTO | | DISTANCIA MÁXIMA |
|---|---|---|
| Elementos superficiales horizontales (losas, forjados, zapatas y losas de cimentación, etc.) | Emparrillado inferior | 50 ∅ > 100 cm |
| | Emparrillado superior | 50 ∅ < 50 cm |
| Muros | Cada emparrillado | 50 ∅ o 50 cm |
| | Separación emparrillados | 100 cm |
| Vigas (1) | | 100 cm |
| Soportes (1) | | 100 ∅ > 200 cm |


(1) Se dispondrán, al menos, tres planos de separadores por vano, en el caso de vigas, y por tramo, en el caso de los soportes, acoplados a los cercos o estribos.

∅ Diámetro de la armadura a la que se acople el separador.


### Cargas en Forjados

| SUELO | | CUBIERTA | |
|---|---|---|---|
| Peso propio. | 120 kg/m2 | Peso propio. | 25 kg/m2 |
| Sobrecarga de uso: | 200 kg/m2 | Sobrecarga de uso: | 40 kg/m2 |
| Cargas muertas: | 100 kg/m2 | Nieve: | 20 kg/m2 |
| Carga total (F.U. 25+5) | 420 kg/m2 | Carga total (LOSA 25cm) | 65 kg/m2 |


# Tipo 1

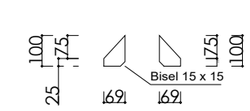



Rigidizadores x - x (e = 6 mm)

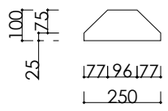



Rigidizadores y - y (e = 6 mm)

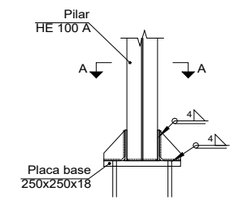



Alzado

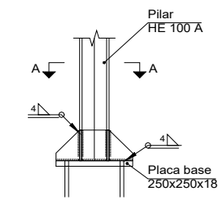


Vista lateral

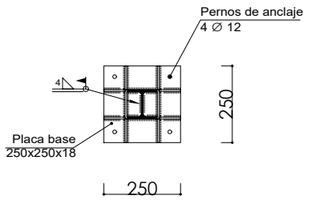


Sección A - A

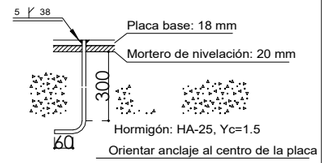


Anclaje de los pernos ∅ 12,
B 400 S, Ys = 1.15 (corrugado)

Escala 1:20

**TINI PERSONALIZADA - SAN LLUIS - PINO**

PROYECTO DE IMPLANTACION

UBICACIÓN: AV. SON REMI 24, 07713, SANT LLUIS
FECHA: AGOSTO 2024
ESCALA: Como se indica
CAPÍTULO: ARQUITECTURA
TÍTULO: DETALLES ESTRUCTURA

E06


PROPIEDAD
Sr./Sra. _____

ARQUITECTO
IGNACIO DE LA VEGA
Nº 22.169 (COAM)
ignacio@tiniliving.com


FORMATO
A3

REVISIÓN
Verificador




TERRAZA DETALLE

1 : 45


**TINI PERSONALIZADA - SAN LLUIS - PINO**

PROYECTO DE IMPLANTACION

| | |
|---|---|
| UBICACIÓN: | AV. SON REMI 24, 07713, SANT LLUIS |
| FECHA: | AGOSTO 2024 |
| ESCALA: | 1 : 45 |
| CAPÍTULO: | ARQUITECTURA |
| TÍTULO: | DETALLE TERRAZA |

E07

| PROPIEDAD | ARQUITECTO | FORMATO | REVISIÓN |
|---|---|---|---|
| Sr./Sra. _____ | IGNACIO DE LA VEGA<br>Nº 22.169 (COAM)<br>ignacio@tiniliving.com | A3 | Verificador |

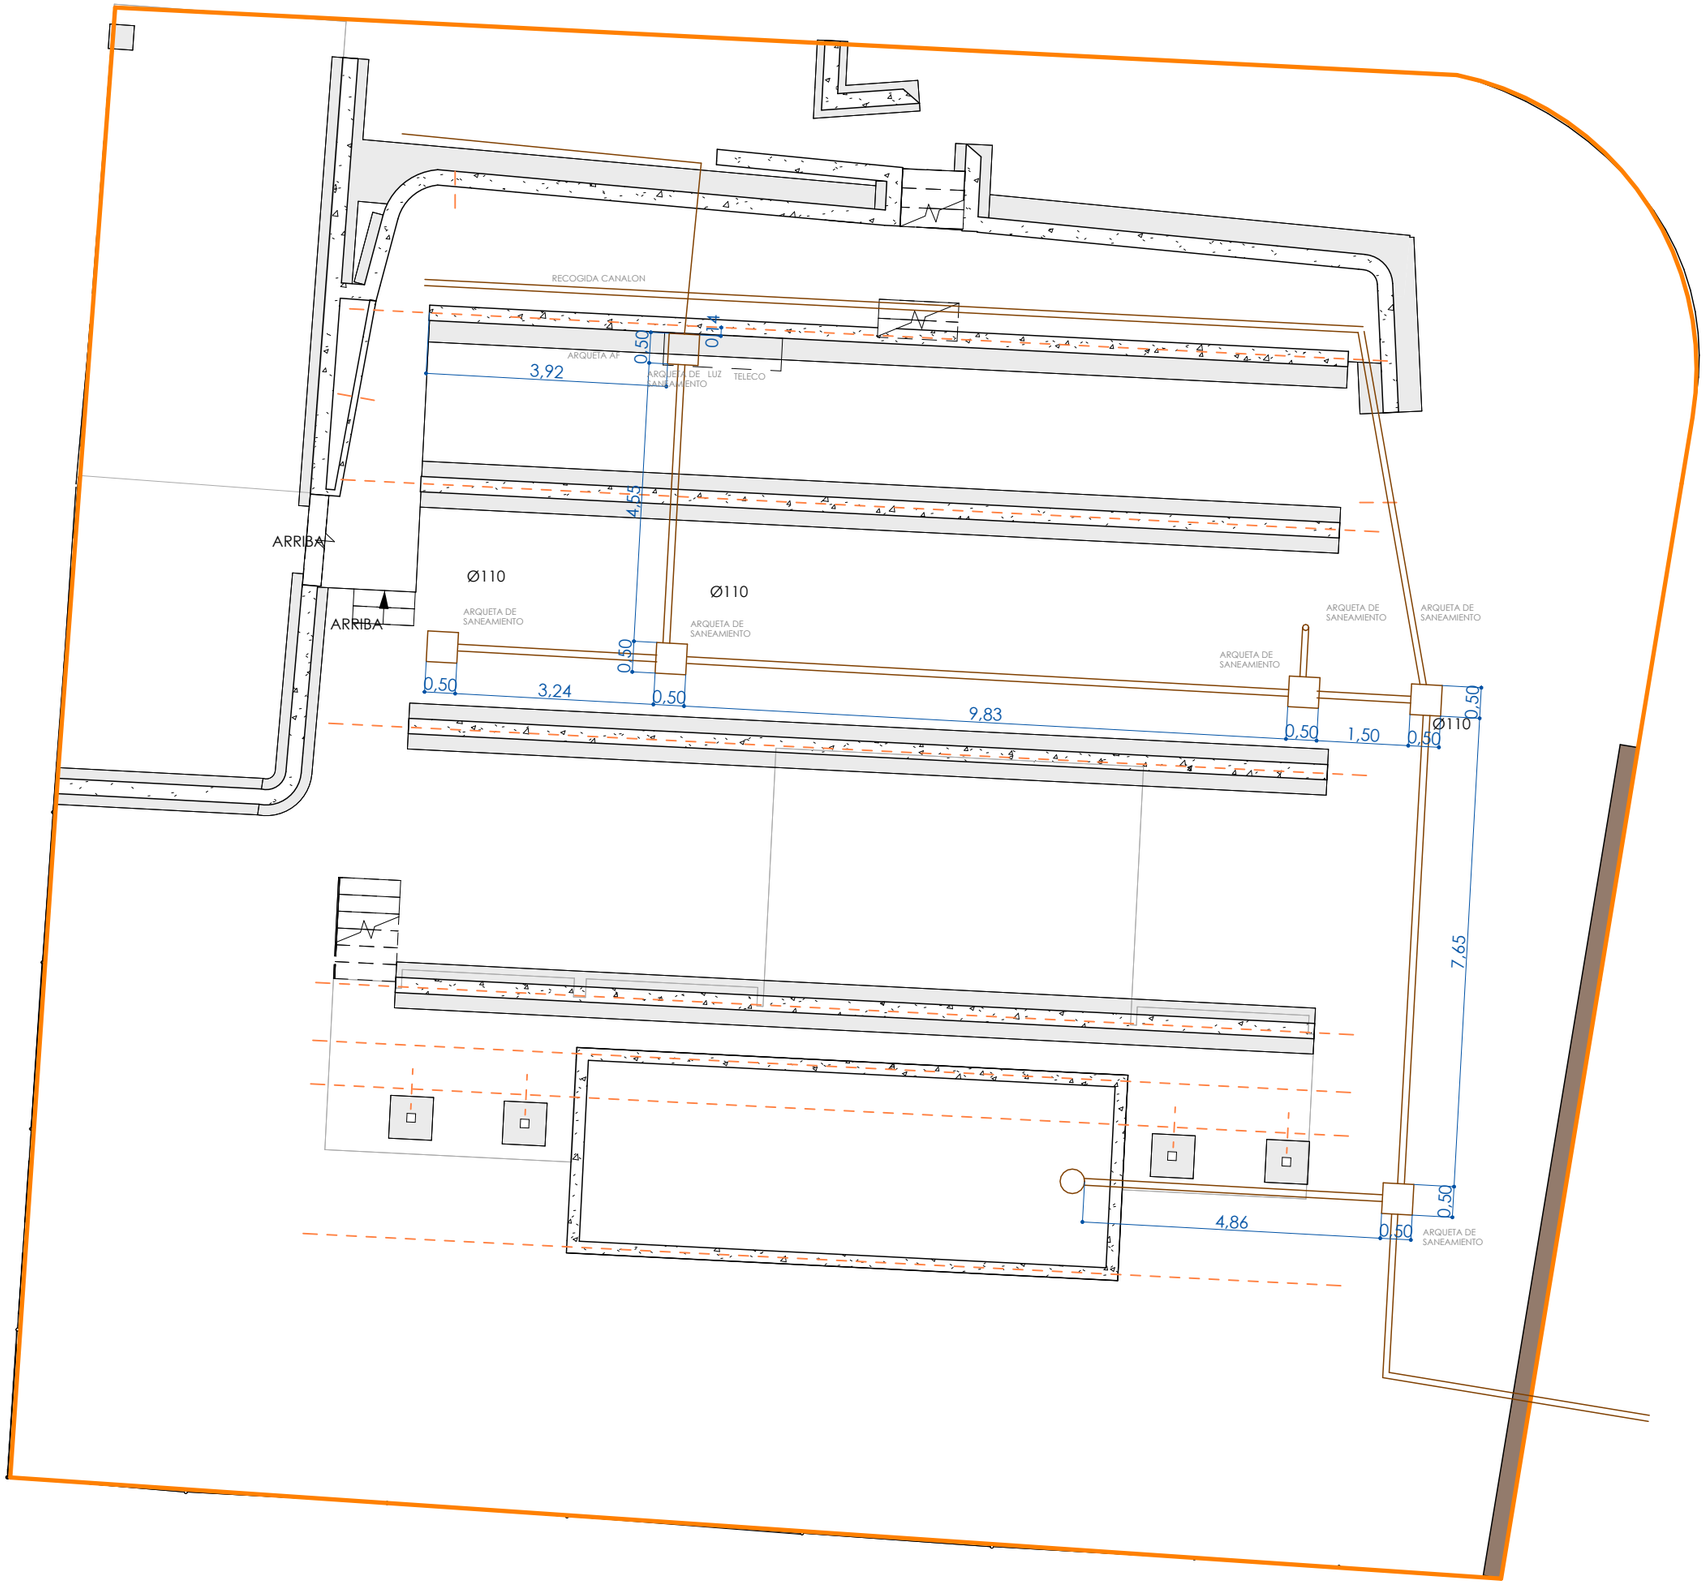


SANEAMIENTO

1 : 100


**TINI PERSONALIZADA - SAN LLUIS - PINO**

PROYECTO DE IMPLANTACION

UBICACIÓN: AV. SON REMI 24, 07713, SANT LLUIS
FECHA: AGOSTO 2024
ESCALA: 1 : 100
CAPÍTULO: ARQUITECTURA
TÍTULO: SANEAMIENTO

I01

| PROPIEDAD | ARQUITECTO | FORMATO | REVISIÓN |
|---|---|---|---|
| Sr./Sra. _____ | IGNACIO DE LA VEGA<br>Nº 22.169 (COAM)<br>ignacio@tiniliving.com | A3 | Verificador |

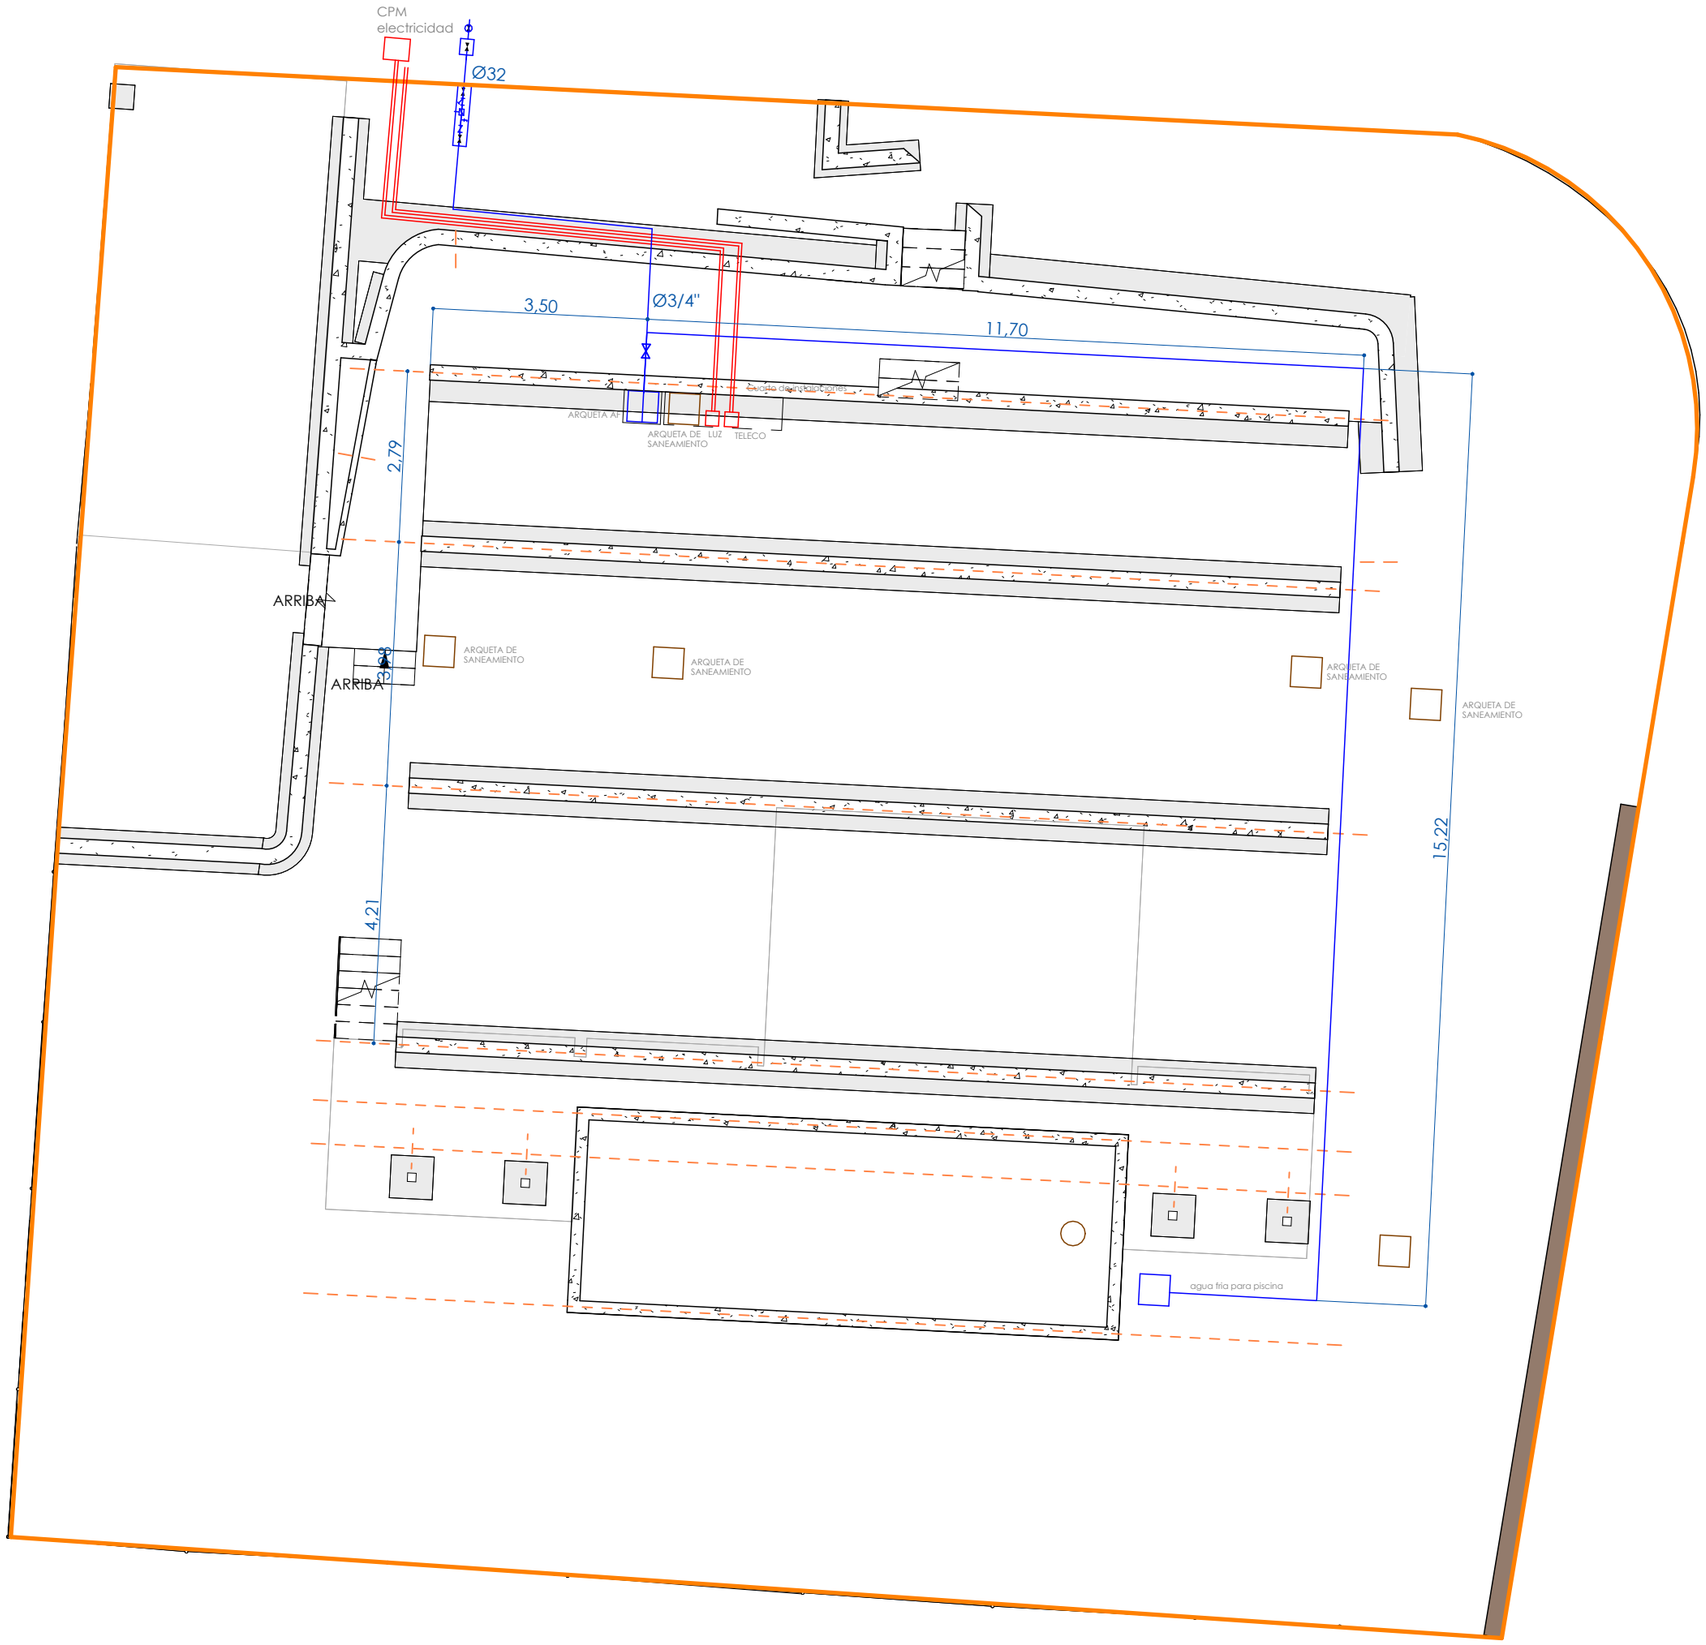


TELECO AGUA ELECTRICIDAD

1 : 100


**TINI PERSONALIZADA - SAN LLUIS - PINO**

PROYECTO DE IMPLANTACION

| | |
|---|---|
| UBICACIÓN: | AV. SON REMI 24, 07713, SANT LLUIS |
| FECHA: | AGOSTO 2024 |
| ESCALA: | 1 : 100 |
| CAPÍTULO: | ARQUITECTURA |
| TÍTULO: | TELECO LUZ AGUA |

I02

| PROPIEDAD | ARQUITECTO | FORMATO | REVISIÓN |
|---|---|---|---|
| Sr./Sra. _____ | IGNACIO DE LA VEGA<br>Nº 22.169 (COAM)<br>ignacio@tiniliving.com | A3 | Verificador |

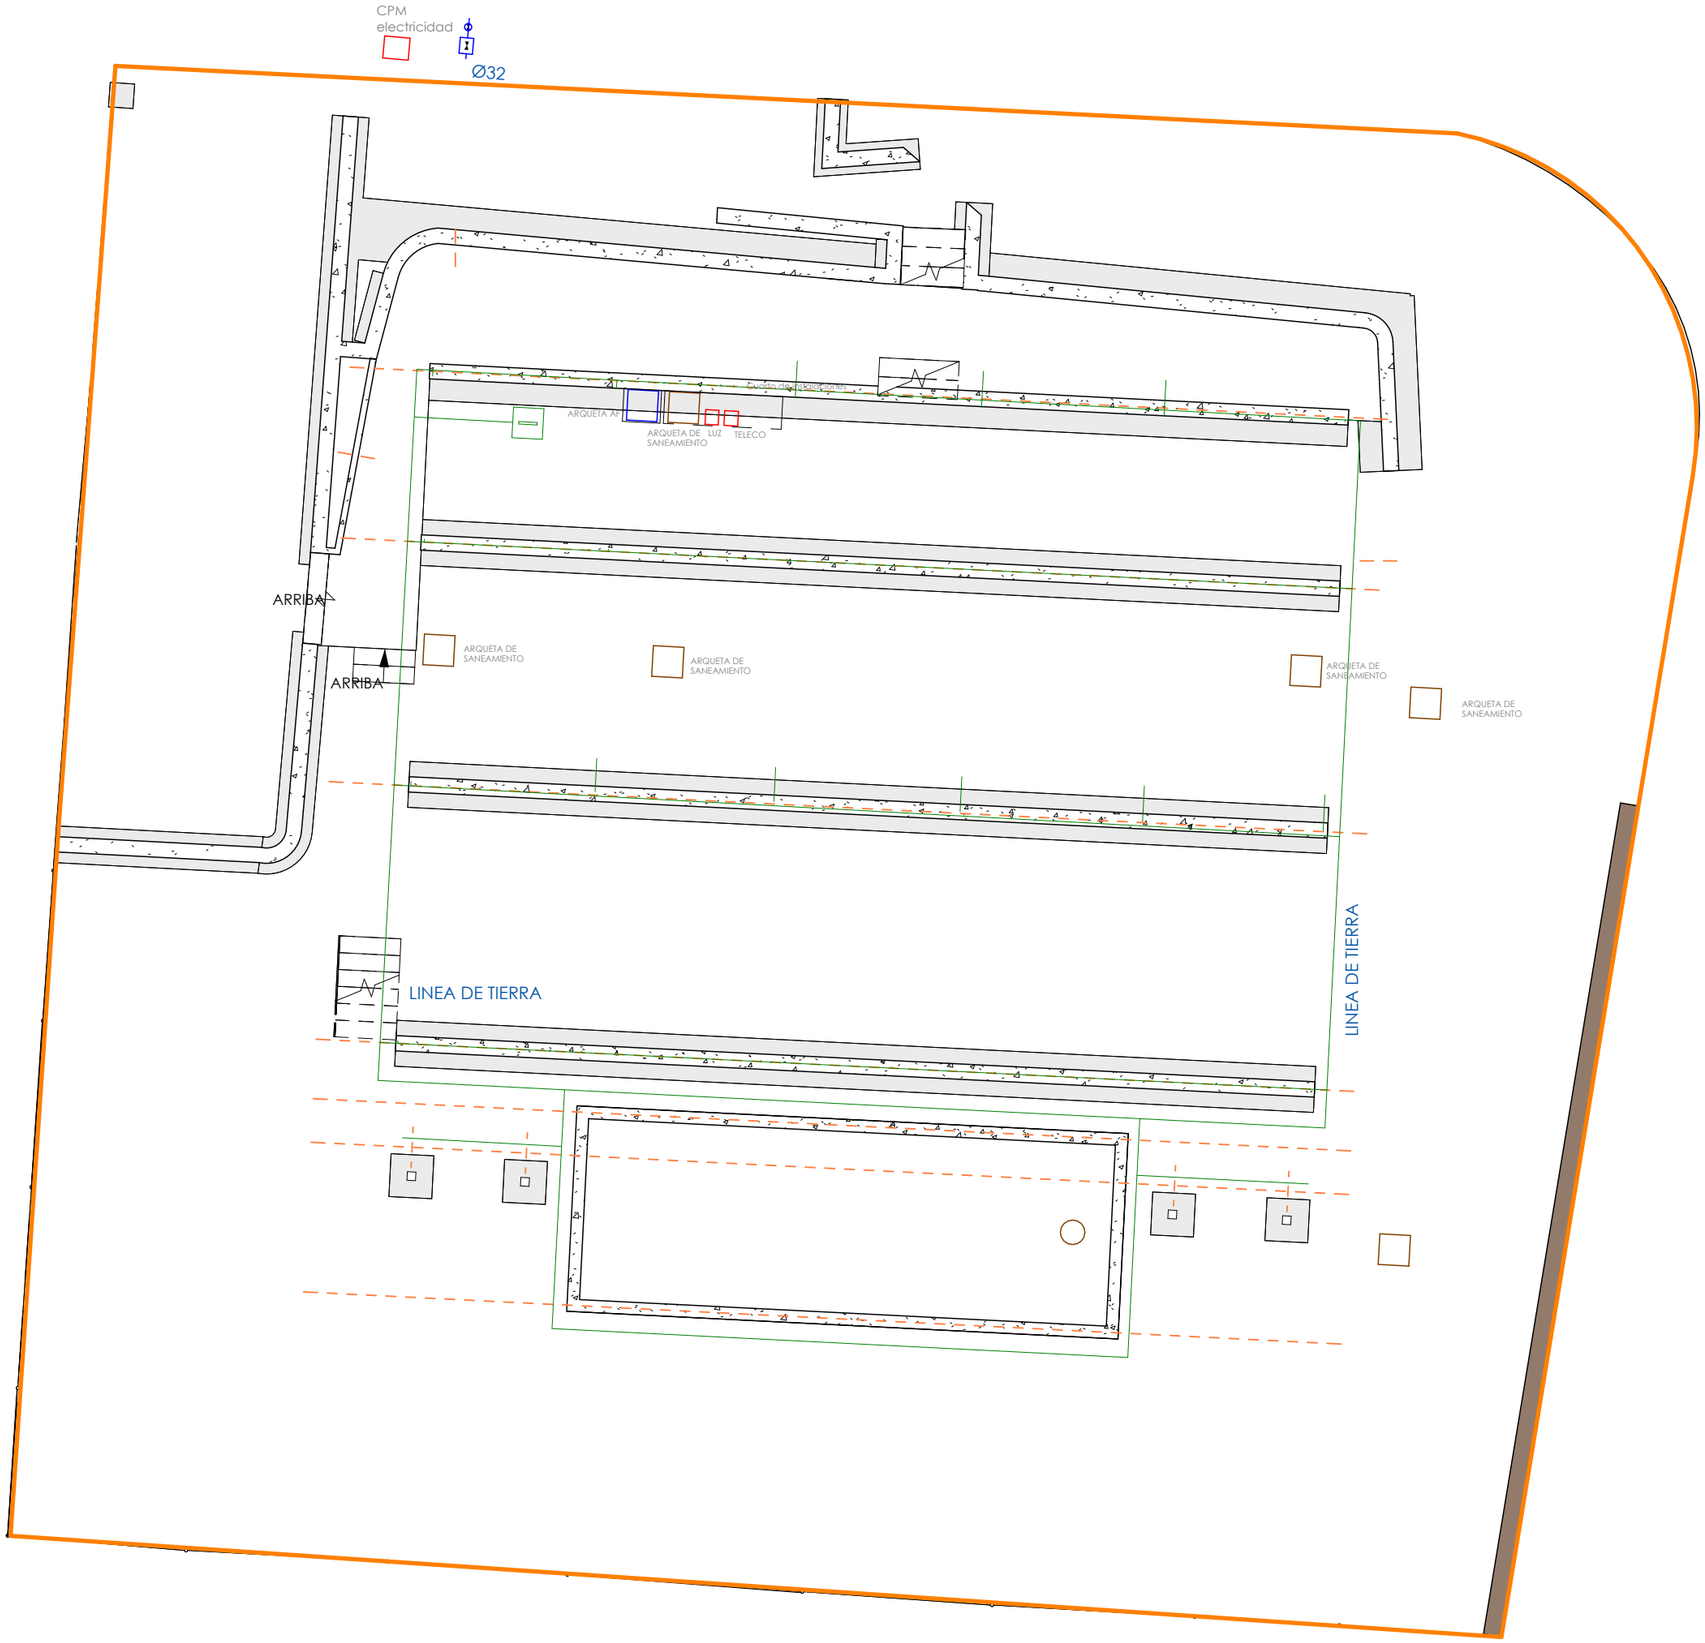


LINEA DE TIERRA

1 : 100


**TINI PERSONALIZADA - SAN LLUIS - PINO**

PROYECTO DE IMPLANTACION

UBICACIÓN: AV. SON REMI 24, 07713, SANT LLUIS
FECHA: AGOSTO 2024
ESCALA: 1 : 100
CAPÍTULO: ARQUITECTURA
TÍTULO: TOMA DE TIERRA

I03

| PROPIEDAD | ARQUITECTO | FORMATO | REVISIÓN |
|---|---|---|---|
| Sr./Sra. _____ | IGNACIO DE LA VEGA<br>Nº 22.169 (COAM)<br>ignacio@tinilliving.com | A3 | Verificador |

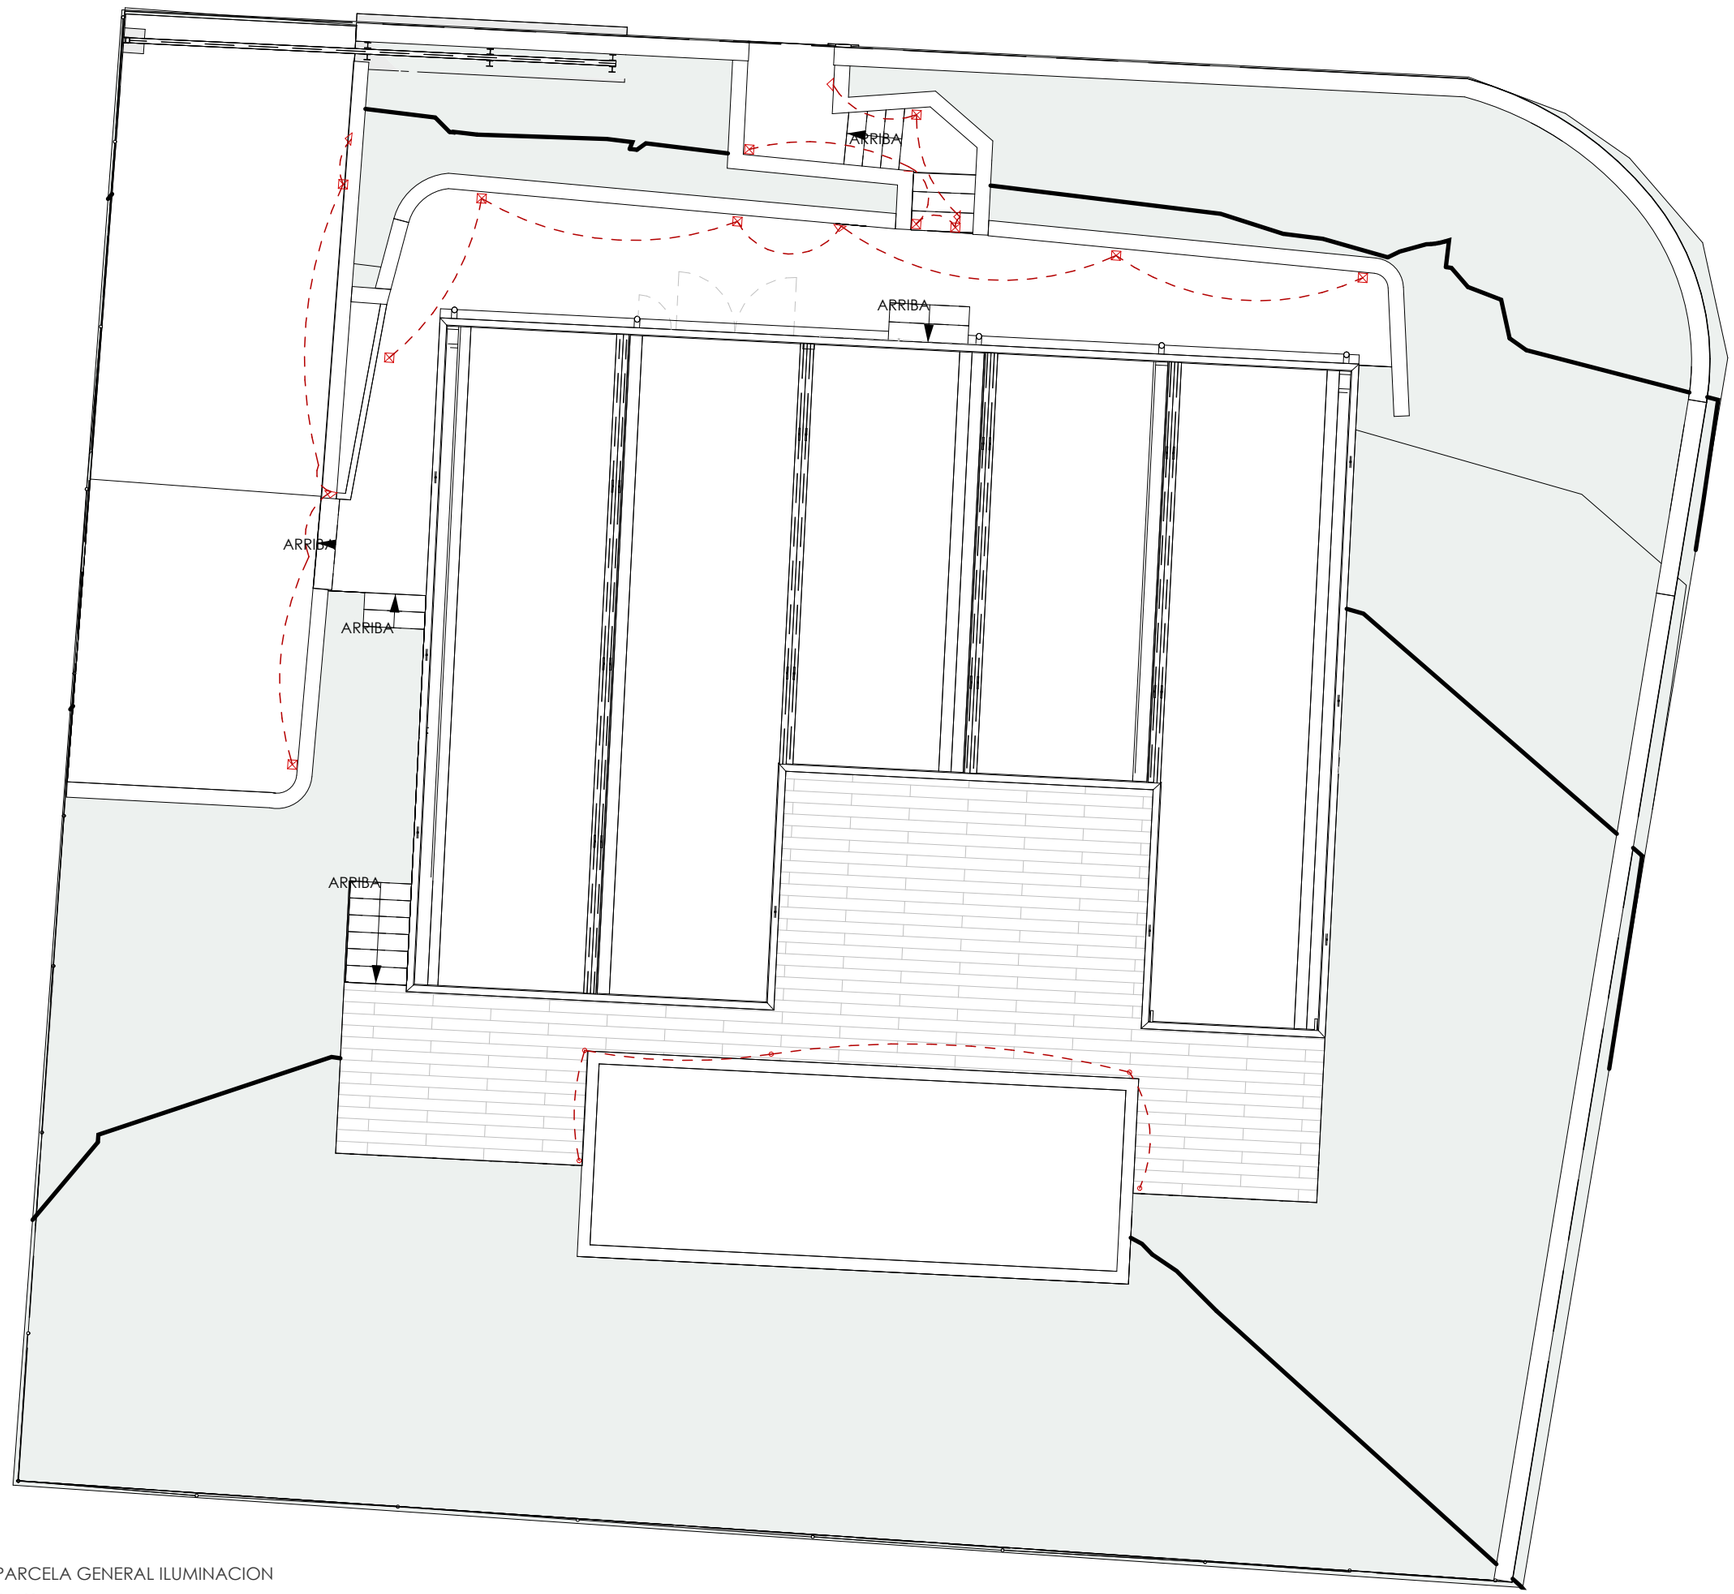


PARCELA GENERAL ILUMINACION

1 : 100

INTERRUPTOR / SIMÓN 270 ESTÉTICA MÍNIMA BLANCO

CONMUTADO / SIMÓN 270 ESTÉTICA MÍNIMA BLANCO

FOCOS PASARELA

FOCOS EXTERIORES EMPOTRADOS A MURO DE HORMIGÓN

DETECTOR DE PRESENCIA


**TINI PERSONALIZADA - SAN LLUIS - PINO**

PROYECTO DE IMPLANTACION

UBICACIÓN: AV. SON REMI 24, 07713, SANT LLUIS
FECHA: AGOSTO 2024
ESCALA: Como se indica
CAPÍTULO: ARQUITECTURA
TÍTULO: ILUMINACION EXTERIOR


I04

| PROPIEDAD | ARQUITECTO | FORMATO | REVISIÓN |
|---|---|---|---|
| Sr./Sra. _____ | IGNACIO DE LA VEGA<br>Nº 22.169 (COAM)<br>ignacio@tiniliving.com | A3 | Verificador |

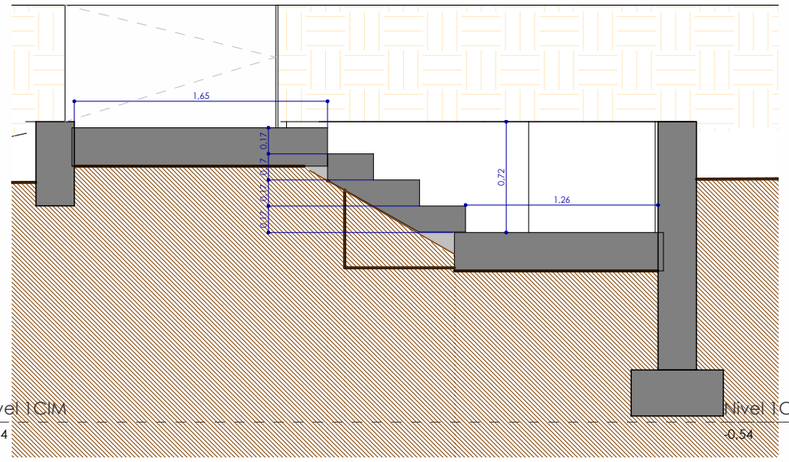



SECCION ACCESo 2

1 : 40

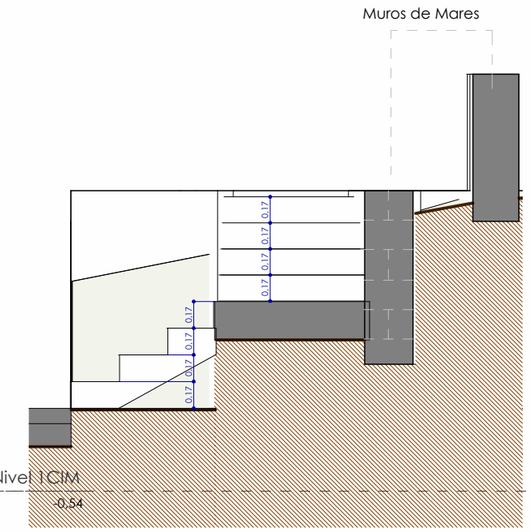



SECCION ACCESO

1 : 40

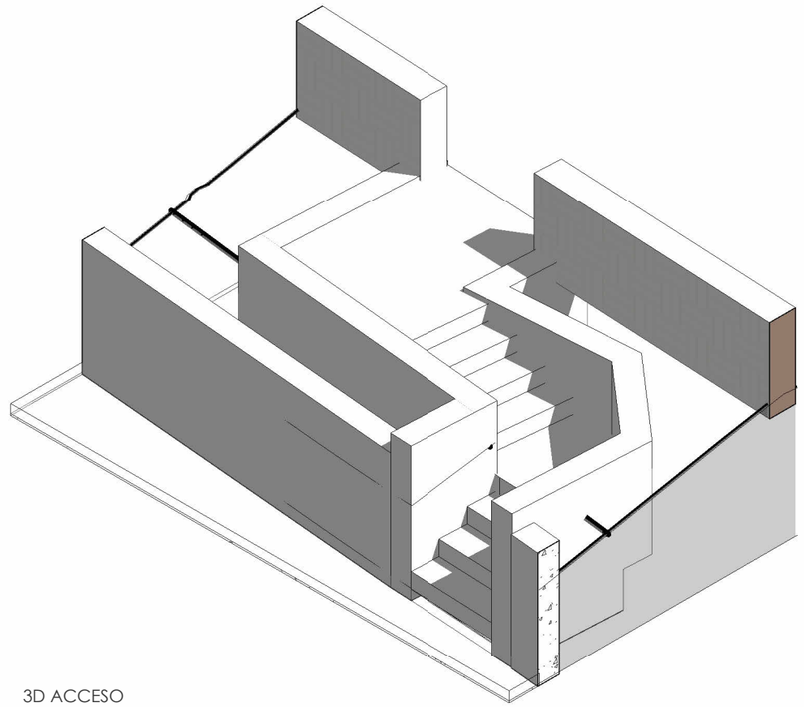

3D ACCESO

Entrada peatonal

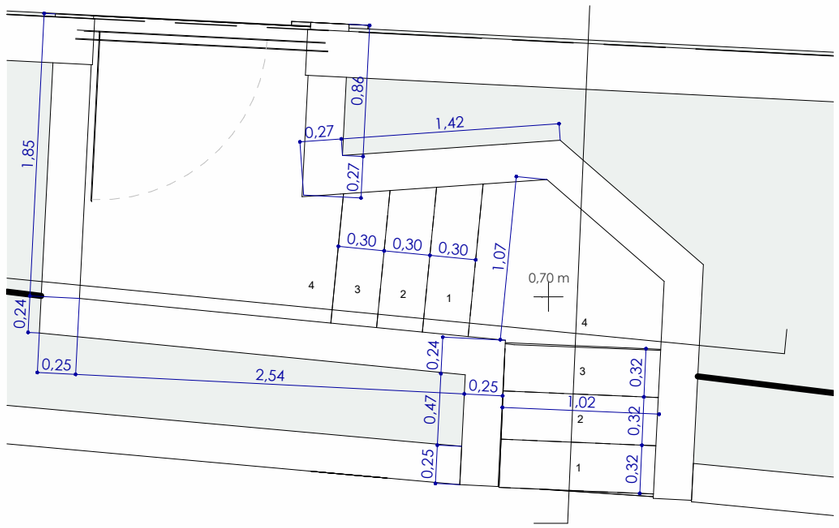


DETALLE ACCESO

1 : 40

**TINI PERSONALIZADA - SAN LLUIS - PINO**

PROYECTO DE IMPLANTACION

UBICACIÓN: AV. SON REMI 24, 07713, SANT LLUIS
FECHA: AGOSTO 2024
ESCALA: 1 : 40
CAPÍTULO: ARQUITECTURA
TÍTULO: ACCESO

I05

| PROPIEDAD | ARQUITECTO | FORMATO | REVISIÓN |
|---|---|---|---|
| Sr./Sra. _____ | IGNACIO DE LA VEGA<br>Nº 22.169 (COAM)<br>ignacio@tinilliving.com | A3 | Verificador |